
TAKE-OFF LEGEND - A2.01 (partition schedule order)

- FI.2-0 - BOARD ONLY (WOOD FRAMING EXCLUDED) - 1 wall(s) - 7.23 LF
- XW.6.2-0 - BOARD ONLY (WOOD FRAMING EXCLUDED) - 1 wall(s) - 9.33 LF
- XW.6.2-2 - BOARD ONLY (WOOD FRAMING EXCLUDED) - 2 wall(s) - 19.82 LF
- XW.6.3-0 - BOARD ONLY (WOOD FRAMING EXCLUDED) - 2 wall(s) - 3.74 LF
- XW.6.3-2 - BOARD ONLY (WOOD FRAMING EXCLUDED) - 2 wall(s) - 38.48 LF
- XW.6.4-2 - BOARD ONLY (WOOD FRAMING EXCLUDED) - 6 wall(s) - 13.88 LF

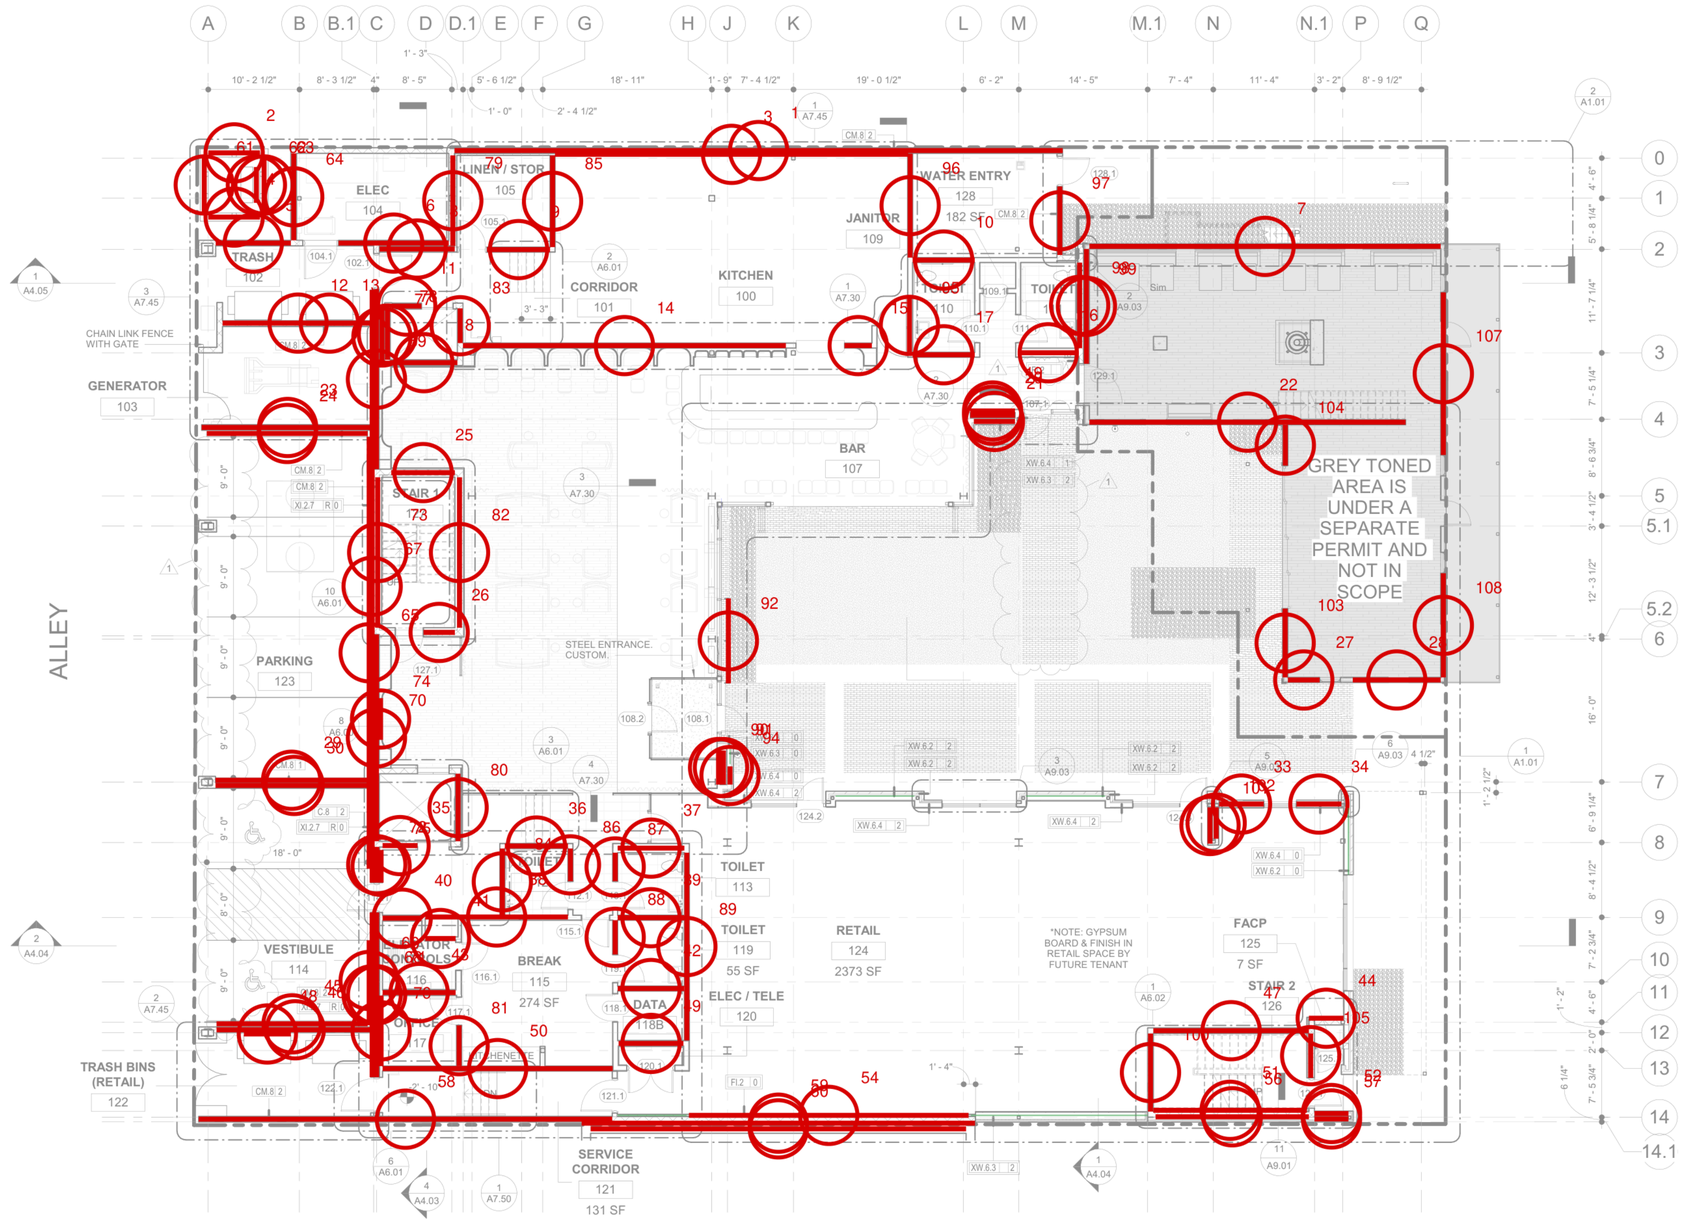

1 LEVEL 1
1/8" = 1'-0"

FLOOR PLAN - GENERAL NOTES

1. DIMENSIONS ARE TO FACE OF STUD/CMU TYP. UON.
2. WHEN "CLEAR" OR "FIN" IS CALLED OUT ON A DIMENSION, PROVIDE DIMENSION NOTED FROM FACE OF FINISH TO FACE OF FINISH.
3. DIMENSION FROM EDGE OF DOOR FRAME TO EDGE OF ADJACENT PERPENDICULAR WALL FINISH SHALL BE 4" UON.
4. PROVIDE WATER RESISTANT GYP BD AT TOILET AND LAVATORY AREAS. MAINTAIN FIRE RATING AT ALL PARTITIONS.
5. FRAMING INSTALLER SHALL NOT RELY ON THE LOCATION OF IN-PLACE CONCRETE WHEN PLACING FRAMING AS THERE MAY BE TOLERANCE INACCURACY AND FLUCTUATIONS IN THE CONCRETE. INSTEAD, THE FRAMER SHALL LOCATE FRAMING RELATIVE TO GRID LINES.
6. WINDOW AND DOOR DIMENSIONS ARE TO CENTERLINE OF WINDOWS AND DOORS TYP UON.
7. REFER TO WALL ASSEMBLY PAGES FOR WALL ASSEMBLY INFO.
8. REFER TO CODE ANALYSIS SHEETS FOR EXITING INFO.
9. REFER TO ACCESSABILITY STANDARDS FOR ACCESSABILITY NOTES
10. REFER TO ENLARGED PLANS FOR DETAILED DIMENSIONS, NOTES, WALL & DOOR TAGS.

INTERIOR WALL ASSEMBLIES - LEGEND

1. REFERENCE LEGEND, RE: FLOOR PLANS

W.6 | 1

PARTITION TYPE -
- FIRST POSITION INDICATES INTERIOR PARTITION TYPE AND MATERIAL DESIGNATION.
- SECOND POSITION INDICATES RELATIVE WIDTH OF PARTITION.
- THIRD POSITION INDICATES FIRE RATING.

W.6 | 1

DOUBLE LINES INDICATES ACOUSTICAL PARTITION - IDENTICAL TO DESIGNATED PARTITION TYPE EXCEPT WITH ACOUSTICAL INSULATION AND ACOUSTICAL SEALANT AT PERIMETER AND PENETRATIONS.

PARTITION - PARTITION REFERENCE SYMBOL IS ORIENTED TO DENOTED PARTITION ON SAME SIDE AS DELINEATED IN PARTITION DETAIL.

EXTERIOR WALL ASSEMBLIES - LEGEND

1. REFERENCE LEGEND, RE: FLOOR PLANS

XM.6.12 R 1

PARTITION TYPE -
- FIRST POSITION INDICATES EXTERIOR PARTITION TYPE AND MATERIAL DESIGNATION.
- SECOND POSITION INDICATES STUD WIDTH.
- THIRD POSITION INDICATES FINISH MATERIAL.
- "R" AFTER THIRD POSITION INDICATES CONTINUOUS RIGID INSULATION REQUIRED.
- FOURTH POSITION INDICATES FIRE RATING IN HOURS.

XM.6.12 R 1

DOUBLE LINES INDICATE PARTITIONS WHICH SHALL INCORPORATE THE INSULATION REQUIREMENTS NOTED IN THE WALL TYPE DETAILS. ADDITIONALLY, THESE PARTITIONS INCORPORATE ACOUSTICAL SEALANT AT PERIMETER AND PENETRATIONS.

PARTITION - PARTITION REFERENCE SYMBOL IS ORIENTED TO DENOTED PARTITION ON SAME SIDE AS DELINEATED IN PARTITION DETAIL.

2. FINISH MATERIALS

.1	NO FINISH
.2	BRICK
.3	WOOD - GREY
.4	WOOD - BLACK
.5	WOOD W/VERTICAL BATTENS - BLACK
.6	FRT WOOD W/VERTICAL BATTENS - BLACK
.7	FRP (FIBER-REINFORCED PLASTIC)
.8	WOOD - WHITE

C:\Users\daniel\Documents\City Hotel-2024_1_dfpscomb74CJ8.rvt

4/22/2026 1:06:20 PM

HELTSHE


M1A MERIDIAN 105 ARCHITECTURE

CITY HOTEL
415 PERRY STREET, CASTLE ROCK, CO.

DATE: 4.22.2026	ISSUED FOR: PERMIT	SHEET TITLE: LVL 1	SHEET NUMBER A2.01
PROJ. NO. 2023.002			

TAKE-OFF LEGEND - A2.02 (partition schedule order)

- CH.6-2 - SHAFT WALL (C-H STUDS AND J-RUNNER IN THE MATERIAL SUMMARY) - 14 wall(s) - 49.12 LF
- DW.4-1 - BOARD ONLY (WOOD FRAMING EXCLUDED) - 36 wall(s) - 463.46 LF
- FI.2-0 - BOARD ONLY (WOOD FRAMING EXCLUDED) - 3 wall(s) - 33.85 LF
- FI.6-0 - BOARD ONLY (WOOD FRAMING EXCLUDED) - 5 wall(s) - 86.18 LF
- FW.2-0 - BOARD ONLY (WOOD FRAMING EXCLUDED) - 15 wall(s) - 118.59 LF
- FW.4-0 - BOARD ONLY (WOOD FRAMING EXCLUDED) - 41 wall(s) - 149.93 LF
- FW.6-0 - BOARD ONLY (WOOD FRAMING EXCLUDED) - 2 wall(s) - 22.28 LF
- W.4-0 - BOARD ONLY (WOOD FRAMING EXCLUDED) - 112 wall(s) - 598.60 LF
- W.6-0 - BOARD ONLY (WOOD FRAMING EXCLUDED) - 5 wall(s) - 11.90 LF
- W.6-2 - BOARD ONLY (WOOD FRAMING EXCLUDED) - 1 wall(s) - 5.04 LF
- W.62-1 - BOARD ONLY (WOOD FRAMING EXCLUDED) - 54 wall(s) - 626.73 LF
- XW.6.3-0 - BOARD ONLY (WOOD FRAMING EXCLUDED) - 1 wall(s) - 65.99 LF
- XW.6.3-2 - BOARD ONLY (WOOD FRAMING EXCLUDED) - 32 wall(s) - 672.39 LF
- XW.6.4-0 - BOARD ONLY (WOOD FRAMING EXCLUDED) - 1 wall(s) - 19.43 LF
- XW.6.4-2 - BOARD ONLY (WOOD FRAMING EXCLUDED) - 2 wall(s) - 50.98 LF
- XW.6.6-1 - BOARD ONLY (WOOD FRAMING EXCLUDED) - 6 wall(s) - 64.34 LF

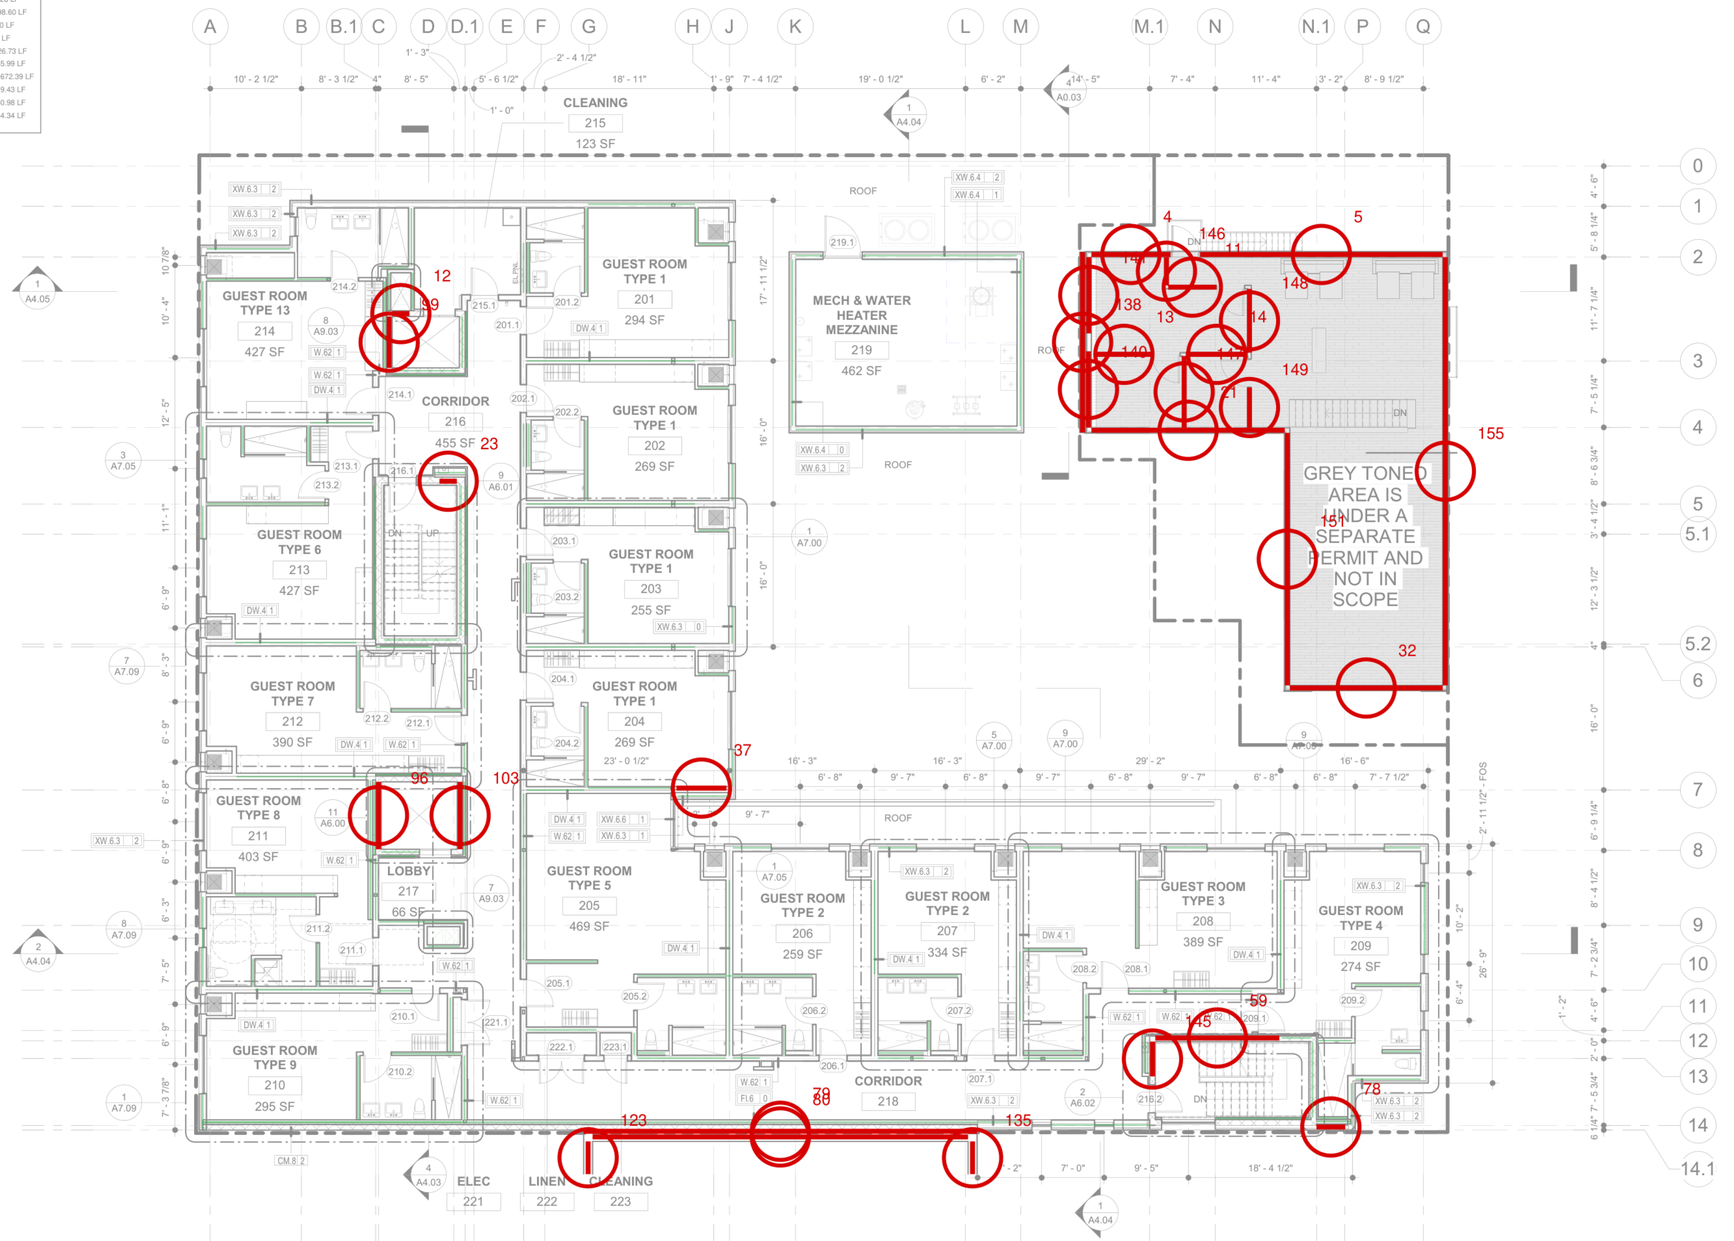

1 LEVEL 2
1/8" = 1'-0"

FLOOR PLAN - GENERAL NOTES

1. DIMENSIONS ARE TO FACE OF STUD/CMU TYP. UON.
2. WHEN "CLEAR" OR "FIN" IS CALLED OUT ON A DIMENSION, PROVIDE DIMENSION NOTED FROM FACE OF FINISH TO FACE OF FINISH.
3. DIMENSION FROM EDGE OF DOOR FRAME TO EDGE OF ADJACENT PERPENDICULAR WALL FINISH SHALL BE 4" UON.
4. PROVIDE WATER RESISTANT GYP BD AT TOILET AND LAVATORY AREAS. MAINTAIN FIRE RATING AT ALL PARTITIONS.
5. FRAMING INSTALLER SHALL NOT RELY ON THE LOCATION OF IN-PLACE CONCRETE WHEN PLACING FRAMING AS THERE MAY BE TOLERANCE INACCURACY AND FLUCTUATIONS IN THE CONCRETE. INSTEAD, THE FRAMER SHALL LOCATE FRAMING RELATIVE TO GRID LINES.
6. WINDOW AND DOOR DIMENSIONS ARE TO CENTERLINE OF WINDOWS AND DOORS TYP UON.
7. REFER TO WALL ASSEMBLY PAGES FOR WALL ASSEMBLY INFO.
8. REFER TO CODE ANALYSIS SHEETS FOR EXITING INFO.
9. REFER TO ACCESSABILITY STANDARDS FOR ACCESSABILITY NOTES
10. REFER TO ENLARGED PLANS FOR DETAILED DIMENSIONS, NOTES, WALL & DOOR TAGS.

INTERIOR WALL ASSEMBLIES - LEGEND

1. REFERENCE LEGEND, RE: FLOOR PLANS

W.6 1

PARTITION TYPE -
- FIRST POSITION INDICATES INTERIOR PARTITION TYPE AND MATERIAL DESIGNATION.
- SECOND POSITION INDICATES RELATIVE WIDTH OF PARTITION.
- THIRD POSITION INDICATES FIRE RATING.

W.6 1

DOUBLE LINES INDICATES ACOUSTICAL PARTITION - IDENTICAL TO DESIGNATED PARTITION TYPE EXCEPT WITH ACOUSTICAL INSULATION AND ACOUSTICAL SEALANT AT PERIMETER AND PENETRATIONS.

PARTITION - PARTITION REFERENCE SYMBOL IS ORIENTED TO DENOTED PARTITION ON SAME SIDE AS DELINEATED IN PARTITION DETAIL.

EXTERIOR WALL ASSEMBLIES - LEGEND

1. REFERENCE LEGEND, RE: FLOOR PLANS

XM.6.12 R 1

PARTITION TYPE -
- FIRST POSITION INDICATES EXTERIOR PARTITION TYPE AND MATERIAL DESIGNATION.
- SECOND POSITION INDICATES STUD WIDTH.
- THIRD POSITION INDICATES FINISH MATERIAL.
- "R" AFTER THIRD POSITION INDICATES CONTINUOUS RIGID INSULATION REQUIRED.
- FOURTH POSITION INDICATES FIRE RATING IN HOURS.

XM.6.12 R 1

DOUBLE LINES INDICATE PARTITIONS WHICH SHALL INCORPORATE THE INSULATION REQUIREMENTS NOTED IN THE WALL TYPE DETAILS. ADDITIONALLY, THESE PARTITIONS INCORPORATE ACOUSTICAL SEALANT AT PERIMETER AND PENETRATIONS.

PARTITION - PARTITION REFERENCE SYMBOL IS ORIENTED TO DENOTED PARTITION ON SAME SIDE AS DELINEATED IN PARTITION DETAIL.

2. FINISH MATERIALS

.1	NO FINISH
.2	BRICK
.3	WOOD - GREY
.4	WOOD - BLACK
.5	WOOD W/VERTICAL BATTENS - BLACK
.6	FRT WOOD W/VERTICAL BATTENS - BLACK
.7	FRP (FIBER-REINFORCED PLASTIC)
.8	WOOD - WHITE

C:\Users\daniel\Documents\City Hotel-2024_1_dlipscomb74CJ8.rvt

4/22/2026 1:06:25 PM

HELTSHE | M1A MERIDIAN 105 ARCHITECTURE


CITY HOTEL
415 PERRY STREET, CASTLE ROCK, CO.

DATE: 4.22.2026
PROJ. NO. 2023.002
ISSUED FOR: PERMIT
SHEET TITLE: LVL 2

SHEET NUMBER
A2.02

TAKE-OFF LEGEND - A2.03 (partition schedule order)

- CH.6-2 - SHAFT WALL (C-H STUDS AND J-RUNNER IN THE MATERIAL SUMMARY) - 14 wall(s) - 49.12 LF
- DW.4-1 - BOARD ONLY (WOOD FRAMING EXCLUDED) - 38 wall(s) - 454.22 LF
- FI.2-0 - BOARD ONLY (WOOD FRAMING EXCLUDED) - 3 wall(s) - 34.66 LF
- FI.6-0 - BOARD ONLY (WOOD FRAMING EXCLUDED) - 4 wall(s) - 88.38 LF
- FW.2-0 - BOARD ONLY (WOOD FRAMING EXCLUDED) - 13 wall(s) - 119.91 LF
- FW.4-0 - BOARD ONLY (WOOD FRAMING EXCLUDED) - 33 wall(s) - 108.04 LF
- FW.6-0 - BOARD ONLY (WOOD FRAMING EXCLUDED) - 9 wall(s) - 53.20 LF
- W.4-0 - BOARD ONLY (WOOD FRAMING EXCLUDED) - 109 wall(s) - 593.76 LF
- W.6-0 - BOARD ONLY (WOOD FRAMING EXCLUDED) - 4 wall(s) - 11.53 LF
- W.6-2 - BOARD ONLY (WOOD FRAMING EXCLUDED) - 1 wall(s) - 5.03 LF
- W.62-1 - BOARD ONLY (WOOD FRAMING EXCLUDED) - 54 wall(s) - 608.40 LF
- XW.6.3-0 - BOARD ONLY (WOOD FRAMING EXCLUDED) - 2 wall(s) - 73.01 LF
- XW.6.3-2 - BOARD ONLY (WOOD FRAMING EXCLUDED) - 30 wall(s) - 623.41 LF
- XW.6.6-0 - BOARD ONLY (WOOD FRAMING EXCLUDED) - 2 wall(s) - 11.56 LF

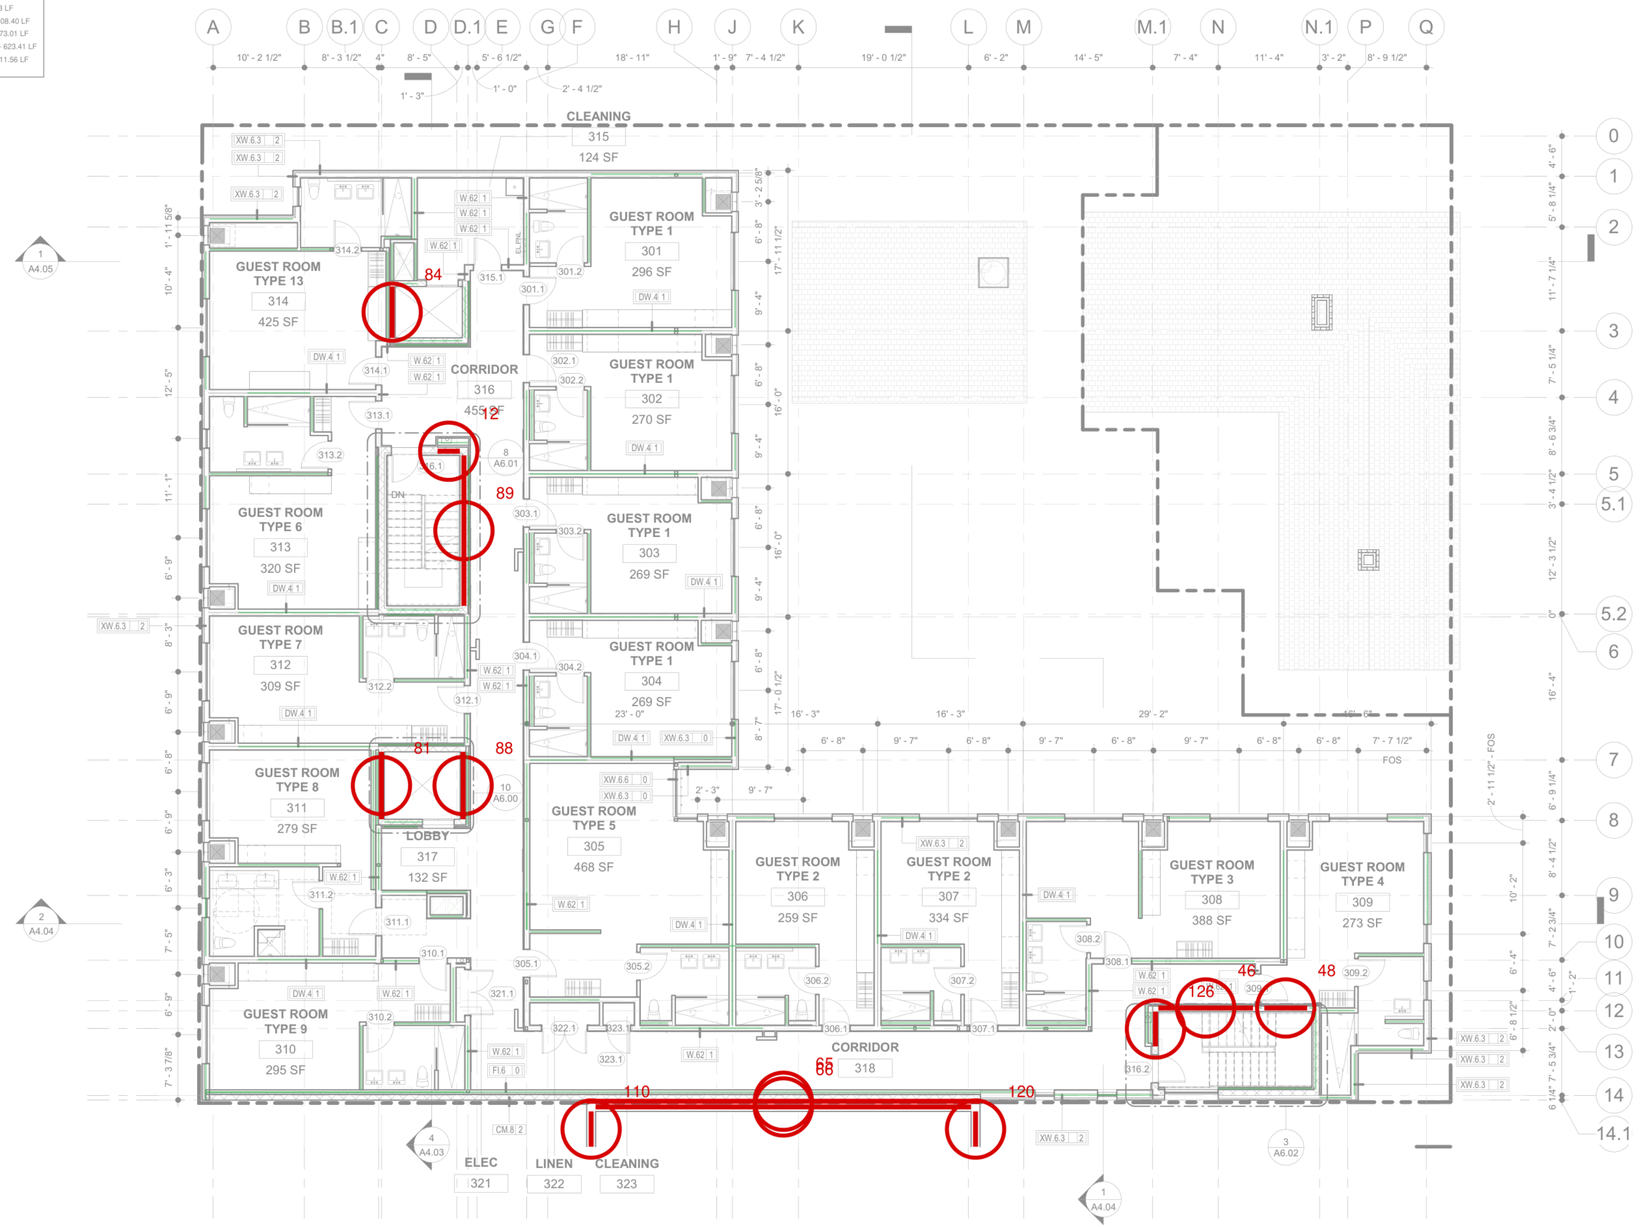

1 LEVEL 3
1/8" = 1'-0"

FLOOR PLAN - GENERAL NOTES

1. DIMENSIONS ARE TO FACE OF STUD/CMU TYP. UON.
2. WHEN "CLEAR" OR "FIN" IS CALLED OUT ON A DIMENSION, PROVIDE DIMENSION NOTED FROM FACE OF FINISH TO FACE OF FINISH.
3. DIMENSION FROM EDGE OF DOOR FRAME TO EDGE OF ADJACENT PERPENDICULAR WALL FINISH SHALL BE 4" UON.
4. PROVIDE WATER RESISTANT GYP BD AT TOILET AND LAVATORY AREAS. MAINTAIN FIRE RATING AT ALL PARTITIONS
5. FRAMING INSTALLER SHALL NOT RELY ON THE LOCATION OF IN-PLACE CONCRETE WHEN PLACING FRAMING AS THERE MAY BE TOLERANCE INACCURACY AND FLUCTUATIONS IN THE CONCRETE. INSTEAD, THE FRAMER SHALL LOCATE FRAMING RELATIVE TO GRID LINES.
6. WINDOW AND DOOR DIMENSIONS ARE TO CENTERLINE OF WINDOWS AND DOORS TYP UON.
7. REFER TO WALL ASSEMBLY PAGES FOR WALL ASSEMBLY INFO.
8. REFER TO CODE ANALYSIS SHEETS FOR EXITING INFO.
9. REFER TO ACCESSABILITY STANDARDS FOR ACCESSABILITY NOTES
10. REFER TO ENLARGED PLANS FOR DETAILED DIMENSIONS, NOTES, WALL & DOOR TAGS.

INTERIOR WALL ASSEMBLIES - LEGEND

1. REFERENCE LEGEND, RE: FLOOR PLANS

W.6 1

PARTITION TYPE -
- FIRST POSITION INDICATES INTERIOR PARTITION TYPE AND MATERIAL DESIGNATION.
- SECOND POSITION INDICATES RELATIVE WIDTH OF PARTITION.
- THIRD POSITION INDICATES FIRE RATING.

W.6 1

DOUBLE LINES INDICATES ACOUSTICAL PARTITION - IDENTICAL TO DESIGNATED PARTITION TYPE EXCEPT WITH ACOUSTICAL INSULATION AND ACOUSTICAL SEALANT AT PERIMETER AND PENETRATIONS.

PARTITION - PARTITION REFERENCE SYMBOL IS ORIENTED TO DENOTED PARTITION ON SAME SIDE AS DELINEATED IN PARTITION DETAIL.

EXTERIOR WALL ASSEMBLIES - LEGEND

1. REFERENCE LEGEND, RE: FLOOR PLANS

XM.6.12 R 1

PARTITION TYPE -
- FIRST POSITION INDICATES EXTERIOR PARTITION TYPE AND MATERIAL DESIGNATION.
- SECOND POSITION INDICATES STUD WIDTH.
- THIRD POSITION INDICATES FINISH MATERIAL.
- "R" AFTER THIRD POSITION INDICATES CONTINUOUS RIGID INSULATION REQUIRED.
- FOURTH POSITION INDICATES FIRE RATING IN HOURS.

XM.6.12 R 1

DOUBLE LINES INDICATE PARTITIONS WHICH SHALL INCORPORATE THE INSULATION REQUIREMENTS NOTED IN THE WALL TYPE DETAILS. ADDITIONALLY, THESE PARTITIONS INCORPORATE ACOUSTICAL SEALANT AT PERIMETER AND PENETRATIONS.

PARTITION - PARTITION REFERENCE SYMBOL IS ORIENTED TO DENOTED PARTITION ON SAME SIDE AS DELINEATED IN PARTITION DETAIL.

2. FINISH MATERIALS

.1 NO FINISH
.2 BRICK
.3 WOOD - GREY
.4 WOOD - BLACK
.5 WOOD W/VERTICAL BATTENS - BLACK
.6 FRT WOOD W/VERTICAL BATTENS - BLACK
.7 FRP (FIBER-REINFORCED PLASTIC)
.8 WOOD - WHITE

C:\Users\daniel\Documents\City Hotel-2024_1_dlipscomb74CJ8.rvt

4/22/2026 1:06:31 PM

HELTSHE | M1A MERIDIAN 105 ARCHITECTURE


CITY HOTEL
415 PERRY STREET, CASTLE ROCK, CO.

DATE: 4.22.2026
PROJ. NO. 2023.002
ISSUED FOR: PERMIT
SHEET TITLE: LVL 3

SHEET NUMBER
A2.03

TAKE-OFF LEGEND - A2.04 (partition schedule order)

- CH.6-2 - SHAFT WALL (C-H STUDS AND J-RUNNER IN THE MATERIAL SUMMARY) - 6 wall(s) - 23.28 LF
- DW.4-1 - BOARD ONLY (WOOD FRAMING EXCLUDED) - 10 wall(s) - 132.43 LF
- FI.6-0 - BOARD ONLY (WOOD FRAMING EXCLUDED) - 1 wall(s) - 60.64 LF
- FW.2-0 - BOARD ONLY (WOOD FRAMING EXCLUDED) - 10 wall(s) - 95.58 LF
- FW.4-0 - BOARD ONLY (WOOD FRAMING EXCLUDED) - 13 wall(s) - 54.06 LF
- FW.4-1 - BOARD ONLY (WOOD FRAMING EXCLUDED) - 2 wall(s) - 24.14 LF
- FW.6-0 - BOARD ONLY (WOOD FRAMING EXCLUDED) - 5 wall(s) - 42.48 LF
- W.4-0 - BOARD ONLY (WOOD FRAMING EXCLUDED) - 31 wall(s) - 216.18 LF
- W.6-0 - BOARD ONLY (WOOD FRAMING EXCLUDED) - 2 wall(s) - 7.28 LF
- W.6-1 - BOARD ONLY (WOOD FRAMING EXCLUDED) - 2 wall(s) - 6.82 LF
- W.62-1 - BOARD ONLY (WOOD FRAMING EXCLUDED) - 19 wall(s) - 227.45 LF
- XW.6.6-0 - BOARD ONLY (WOOD FRAMING EXCLUDED) - 8 wall(s) - 130.56 LF
- XW.6.6-1 - BOARD ONLY (WOOD FRAMING EXCLUDED) - 2 wall(s) - 21.56 LF
- XW.6.6-2 - BOARD ONLY (WOOD FRAMING EXCLUDED) - 27 wall(s) - 399.80 LF

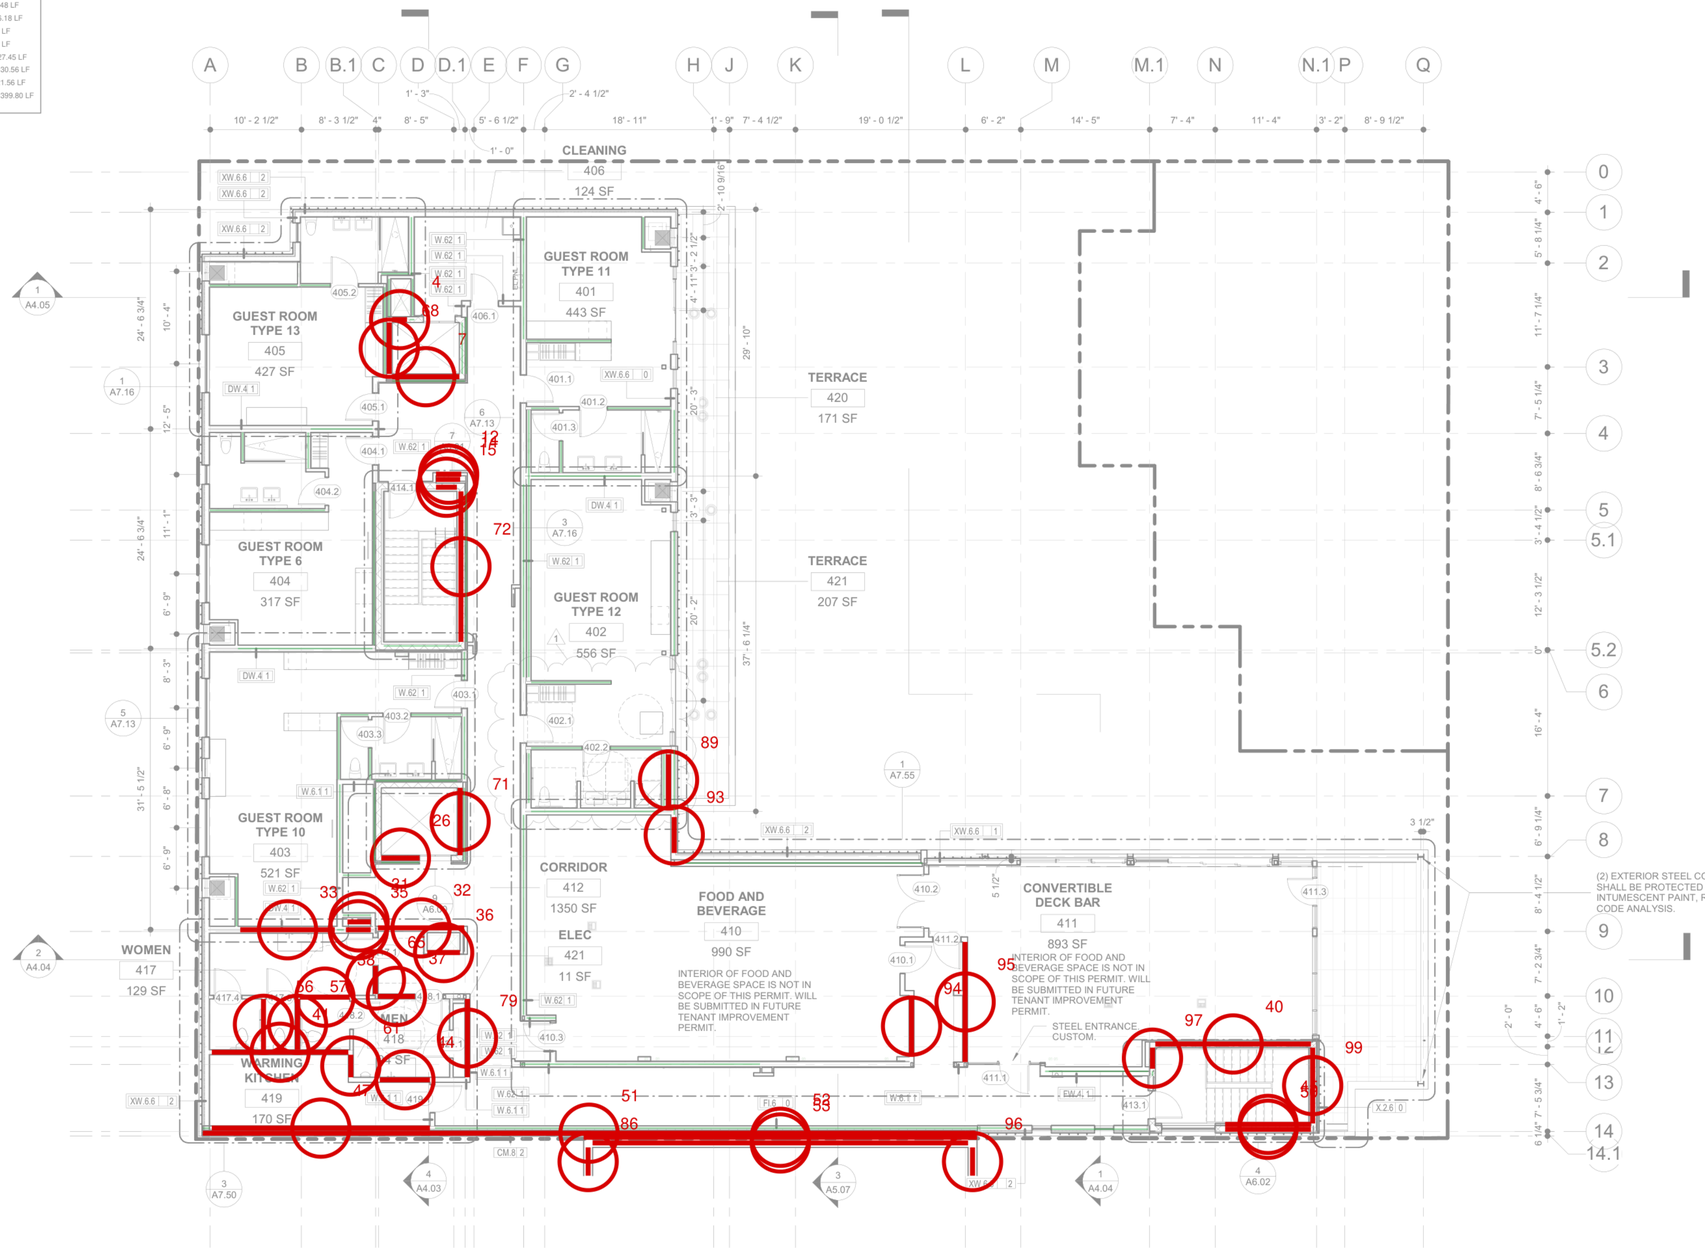


1 LEVEL 4
1/8" = 1'-0"

FLOOR PLAN - GENERAL NOTES

1. DIMENSIONS ARE TO FACE OF STUD/CMU TYP. UON.
2. WHEN "CLEAR" OR "FIN" IS CALLED OUT ON A DIMENSION, PROVIDE DIMENSION NOTED FROM FACE OF FINISH TO FACE OF FINISH.
3. DIMENSION FROM EDGE OF DOOR FRAME TO EDGE OF ADJACENT PERPENDICULAR WALL FINISH SHALL BE 4" UON.
4. PROVIDE WATER RESISTANT GYP BD AT TOILET AND LAVATORY AREAS. MAINTAIN FIRE RATING AT ALL PARTITIONS
5. FRAMING INSTALLER SHALL NOT RELY ON THE LOCATION OF IN-PLACE CONCRETE WHEN PLACING FRAMING AS THERE MAY BE TOLERANCE INACCURACY AND FLUCTUATIONS IN THE CONCRETE. INSTEAD, THE FRAMER SHALL LOCATE FRAMING RELATIVE TO GRID LINES.
6. WINDOW AND DOOR DIMENSIONS ARE TO CENTERLINE OF WINDOWS AND DOORS TYP UON.
7. REFER TO WALL ASSEMBLY PAGES FOR WALL ASSEMBLY INFO.
8. REFER TO CODE ANALYSIS SHEETS FOR EXITING INFO.
9. REFER TO ACCESSABILITY STANDARDS FOR ACCESSABILITY NOTES
10. REFER TO ENLARGED PLANS FOR DETAILED DIMENSIONS, NOTES, WALL & DOOR TAGS.

INTERIOR WALL ASSEMBLIES - LEGEND

1. REFERENCE LEGEND, RE: FLOOR PLANS

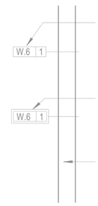

PARTITION TYPE -
- FIRST POSITION INDICATES INTERIOR PARTITION TYPE AND MATERIAL DESIGNATION.
- SECOND POSITION INDICATES RELATIVE WIDTH OF PARTITION.
- THIRD POSITION INDICATES FIRE RATING.

DOUBLE LINES INDICATES ACOUSTICAL PARTITION - IDENTICAL TO DESIGNATED PARTITION TYPE EXCEPT WITH ACOUSTICAL INSULATION AND ACOUSTICAL SEALANT AT PERIMETER AND PENETRATIONS.

PARTITION - PARTITION REFERENCE SYMBOL IS ORIENTED TO DENOTED PARTITION ON SAME SIDE AS DELINEATED IN PARTITION DETAIL.

EXTERIOR WALL ASSEMBLIES - LEGEND

1. REFERENCE LEGEND, RE: FLOOR PLANS

PARTITION TYPE -
- FIRST POSITION INDICATES EXTERIOR PARTITION TYPE AND MATERIAL DESIGNATION.
- SECOND POSITION INDICATES STUD WIDTH.
- THIRD POSITION INDICATES FINISH MATERIAL.
- "R" AFTER THIRD POSITION INDICATES CONTINUOUS RIGID INSULATION REQUIRED.
- FOURTH POSITION INDICATES FIRE RATING IN HOURS.

DOUBLE LINES INDICATE PARTITIONS WHICH SHALL INCORPORATE THE INSULATION REQUIREMENTS NOTED IN THE WALL TYPE DETAILS. ADDITIONALLY, THESE PARTITIONS INCORPORATE ACOUSTICAL SEALANT AT PERIMETER AND PENETRATIONS.

PARTITION - PARTITION REFERENCE SYMBOL IS ORIENTED TO DENOTED PARTITION ON SAME SIDE AS DELINEATED IN PARTITION DETAIL.

2. FINISH MATERIALS

.1 NO FINISH
.2 BRICK
.3 WOOD - GREY
.4 WOOD - BLACK
.5 WOOD W/VERTICAL BATTENS - BLACK
.6 FRT WOOD W/VERTICAL BATTENS - BLACK
.7 FRP (FIBER-REINFORCED PLASTIC)
.8 WOOD - WHITE

HELTSHE | M1A MERIDIAN 105 ARCHITECTURE

CITY HOTEL
415 PERRY STREET, CASTLE ROCK, CO.

DATE: 4.22.2026
PROJ. NO. 2023.002
ISSUED FOR: PERMIT
SHEET TITLE: LVL 4


SHEET NUMBER A2.04

C:\Users\daniel\Documents\City Hotel-2024_1_dfipscomb74CJ8.rvt
4/22/2026 1:06:37 PM

TAKE-OFF LEGEND - A3.01 (gypsum board ceilings / soffits)

blue area = gyp bd ceiling (ceilings), green area / line = gyp bd ceiling / soffit of the misc rows (CLG / SOF / RS / CAN / BW): 8 items, 8,571.45 SF (Contents: board · ceiling tag · room · SF · ceiling height · detail · id)

measure: /Measure at the printed scale of the sheet; SF = Excel row (ceiling id)

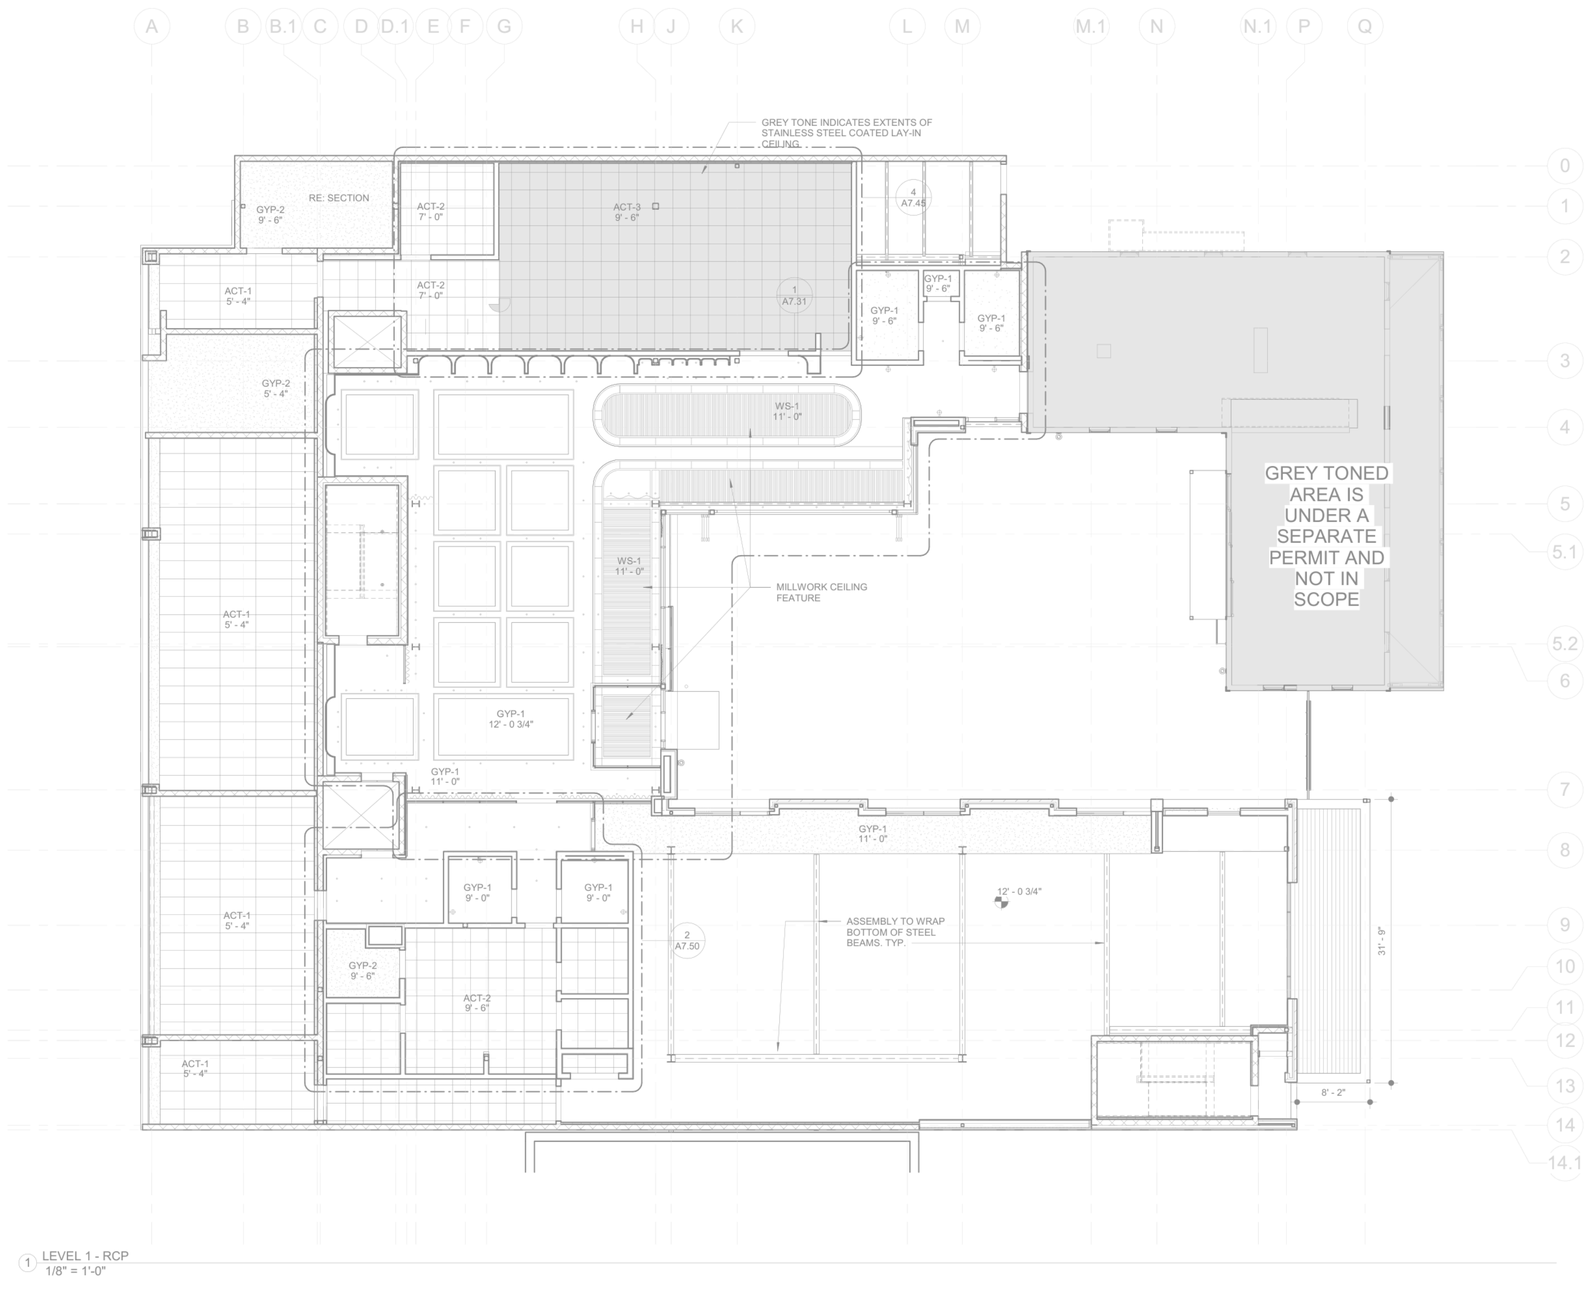

1 LEVEL 1 - RCP
1/8" = 1'-0"

CEILING LEGEND

CEILING TYPES:

ACT-1: 2X4 LAY-IN CEILING, PARKING

ACT-2: 2X2 LAY-IN CEILING, KITCHEN, BACK OF HOUSE

ACT-3: 2X2 LAY-IN CEILING, KITCHEN, WITH METAL FINISH

WS-1: WOOD SLAT CEILING. PRODUCT BY USG INTERIORS 'SPECIALTY CEILING SYSTEM', TRUE WOOD. WOOD VENEER COLOR SELECTED BY ARCHITECT, WITH BLACK FELT REVEAL BACKING. MILLWORK BORDERS AND FLAT PLANAR AREAS TO MATCH FINISH, MATERIAL, AND COLOR OF SLAT PRODUCT.

GYP-1: GYPSUM BOARD ON METAL SUSPENSION SYSTEM, OR WOOD FRAMING

GYP-2: GYPSUM BOARD CEILING, RATED 2-HOURS, AER-09038

NOTE: REFER TO LIGHTING PLANS FOR COMPLETE LAYOUTS AND SPECIFICATIONS OF LIGHTING FIXTURES. DIMENSIONED LOCATION TO BE PROVIDED BY ARCHITECT.

HELTSHE

M1A MERIDIAN 105 ARCHITECTURE

CITY HOTEL
415 PERRY STREET, CASTLE ROCK, CO.

DATE: 4.22.2026
PROJ. NO. 2023.002
ISSUED FOR: PERMIT
SHEET TITLE: OVERALL RCP - LVL 1

SHEET NUMBER
A3.01

C:\Users\daniel\Documents\City Hotel-2024_1_dlipscomb74CJ8.rvt

4/22/2026 1:06:55 PM

TAKE-OFF LEGEND - A3.02 (gypsum board ceilings / soffits)

blue area = gyp bd ceiling (ceilings), green area / line = gyp bd ceiling / soffit of the misc rows (CLG / SOF / RS / CAN / BW): 67 items, 11,489.11 SF (Contents: board · ceiling tag · room · SF · ceiling height · detail · id)

measure: /Measure at the printed scale of the sheet; SF = Excel row (ceiling id)



1 LEVEL 2 - RCP
1/8" = 1'-0"

CEILING LEGEND

CEILING TYPES:

ACT-1: 2X4 LAY-IN CEILING, PARKING

ACT-2: 2X2 LAY-IN CEILING, KITCHEN, BACK OF HOUSE

ACT-3: 2X2 LAY-IN CEILING, KITCHEN, WITH METAL FINISH

WS-1: WOOD SLAT CEILING. PRODUCT BY USG INTERIORS 'SPECIALTY CEILING SYSTEM', TRUE WOOD. WOOD VENEER COLOR SELECTED BY ARCHITECT, WITH BLACK FELT REVEAL BACKING. MILLWORK BORDERS AND FLAT PLANAR AREAS TO MATCH FINISH, MATERIAL, AND COLOR OF SLAT PRODUCT.

GYP-1: GYPSUM BOARD ON METAL SUSPENSION SYSTEM, OR WOOD FRAMING

GYP-2: GYPSUM BOARD CEILING, RATED 2-HOURS, AER-09038

NOTE: REFER TO LIGHTING PLANS FOR COMPLETE LAYOUTS AND SPECIFICATIONS OF LIGHTING FIXTURES. DIMENSIONED LOCATION TO BE PROVIDED BY ARCHITECT.

HELTSHE

M1A MERIDIAN 105 ARCHITECTURE

CITY HOTEL
415 PERRY STREET, CASTLE ROCK, CO.

DATE: 4.22.2026
PROJ. NO. 2023.002

ISSUED FOR: PERMIT

SHEET TITLE: OVERALL RCP - LVL 2

SHEET NUMBER A3.02


C:\Users\daniel\Documents\City Hotel-2024_1_dlipscomb74CJ8.rvt

4/22/2026 1:07:00 PM

TAKE-OFF LEGEND - A3.03 (gypsum board ceilings / soffits)

blue area = gyp bd ceiling (ceilings), green area / line = gyp bd ceiling / soffit of the misc rows (CLG / SOF / RS / CAN / BW): 60 items, 10,561.13 SF (Contents: board · ceiling tag · room · SF · ceiling height · detail · id)

measure: /Measure at the printed scale of the sheet; SF = Excel row (ceiling id)

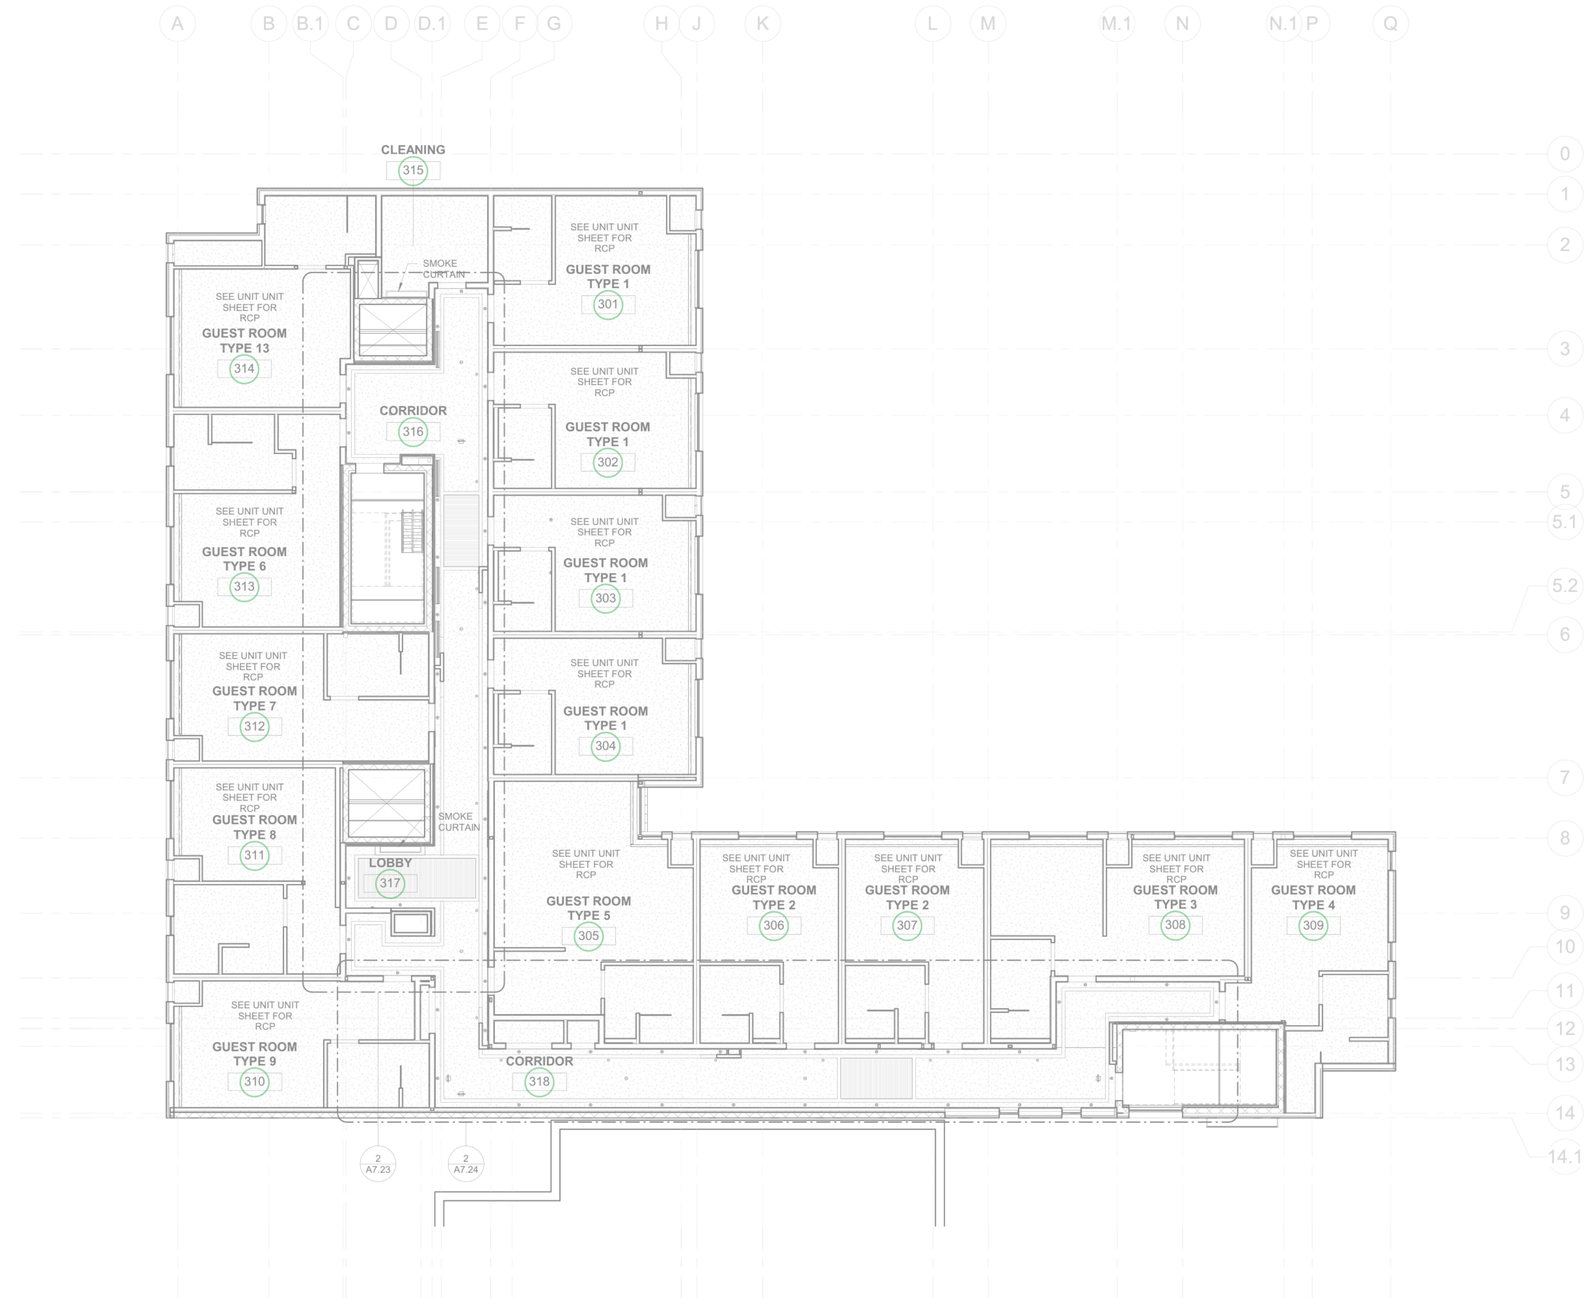

1 LEVEL 3 - RCP
1/8" = 1'-0"

CEILING LEGEND

CEILING TYPES:

ACT-1: 2X4 LAY-IN CEILING, PARKING

ACT-2: 2X2 LAY-IN CEILING, KITCHEN, BACK OF HOUSE

ACT-3: 2X2 LAY-IN CEILING, KITCHEN, WITH METAL FINISH

WS-1: WOOD SLAT CEILING. PRODUCT BY USG INTERIORS 'SPECIALTY CEILING SYSTEM', TRUE WOOD. WOOD VENEER COLOR SELECTED BY ARCHITECT, WITH BLACK FELT REVEAL BACKING. MILLWORK BORDERS AND FLAT PLANAR AREAS TO MATCH FINISH, MATERIAL, AND COLOR OF SLAT PRODUCT.

GYP-1: GYPSUM BOARD ON METAL SUSPENSION SYSTEM, OR WOOD FRAMING

GYP-2: GYPSUM BOARD CEILING, RATED 2-HOURS, AER-09038

NOTE: REFER TO LIGHTING PLANS FOR COMPLETE LAYOUTS AND SPECIFICATIONS OF LIGHTING FIXTURES. DIMENSIONED LOCATION TO BE PROVIDED BY ARCHITECT.

C:\Users\daniel\Documents\City Hotel-2024_1_dlljscomb374CJ8.rvt

4/22/2026 1:07:04 PM

HELTSHE

M1A MERIDIAN 105 ARCHITECTURE

CITY HOTEL
415 PERRY STREET, CASTLE ROCK, CO.

DATE: 4.22.2026
PROJ. NO. 2023.002

ISSUED FOR: PERMIT


SHEET TITLE: OVERALL RCP - LVL 3

SHEET NUMBER A3.03

TAKE-OFF LEGEND - A3.04 (gypsum board ceilings / soffits)

blue area = gyp bd ceiling (ceilings), green area / line = gyp bd ceiling / soffit of the misc rows (CLG / SOF / RS / CAN / BW): 37 items, 5,709.36 SF (Contents: board · ceiling tag · room · SF · ceiling height · detail · id)

measure: /Measure at the printed scale of the sheet; SF = Excel row (ceiling id)

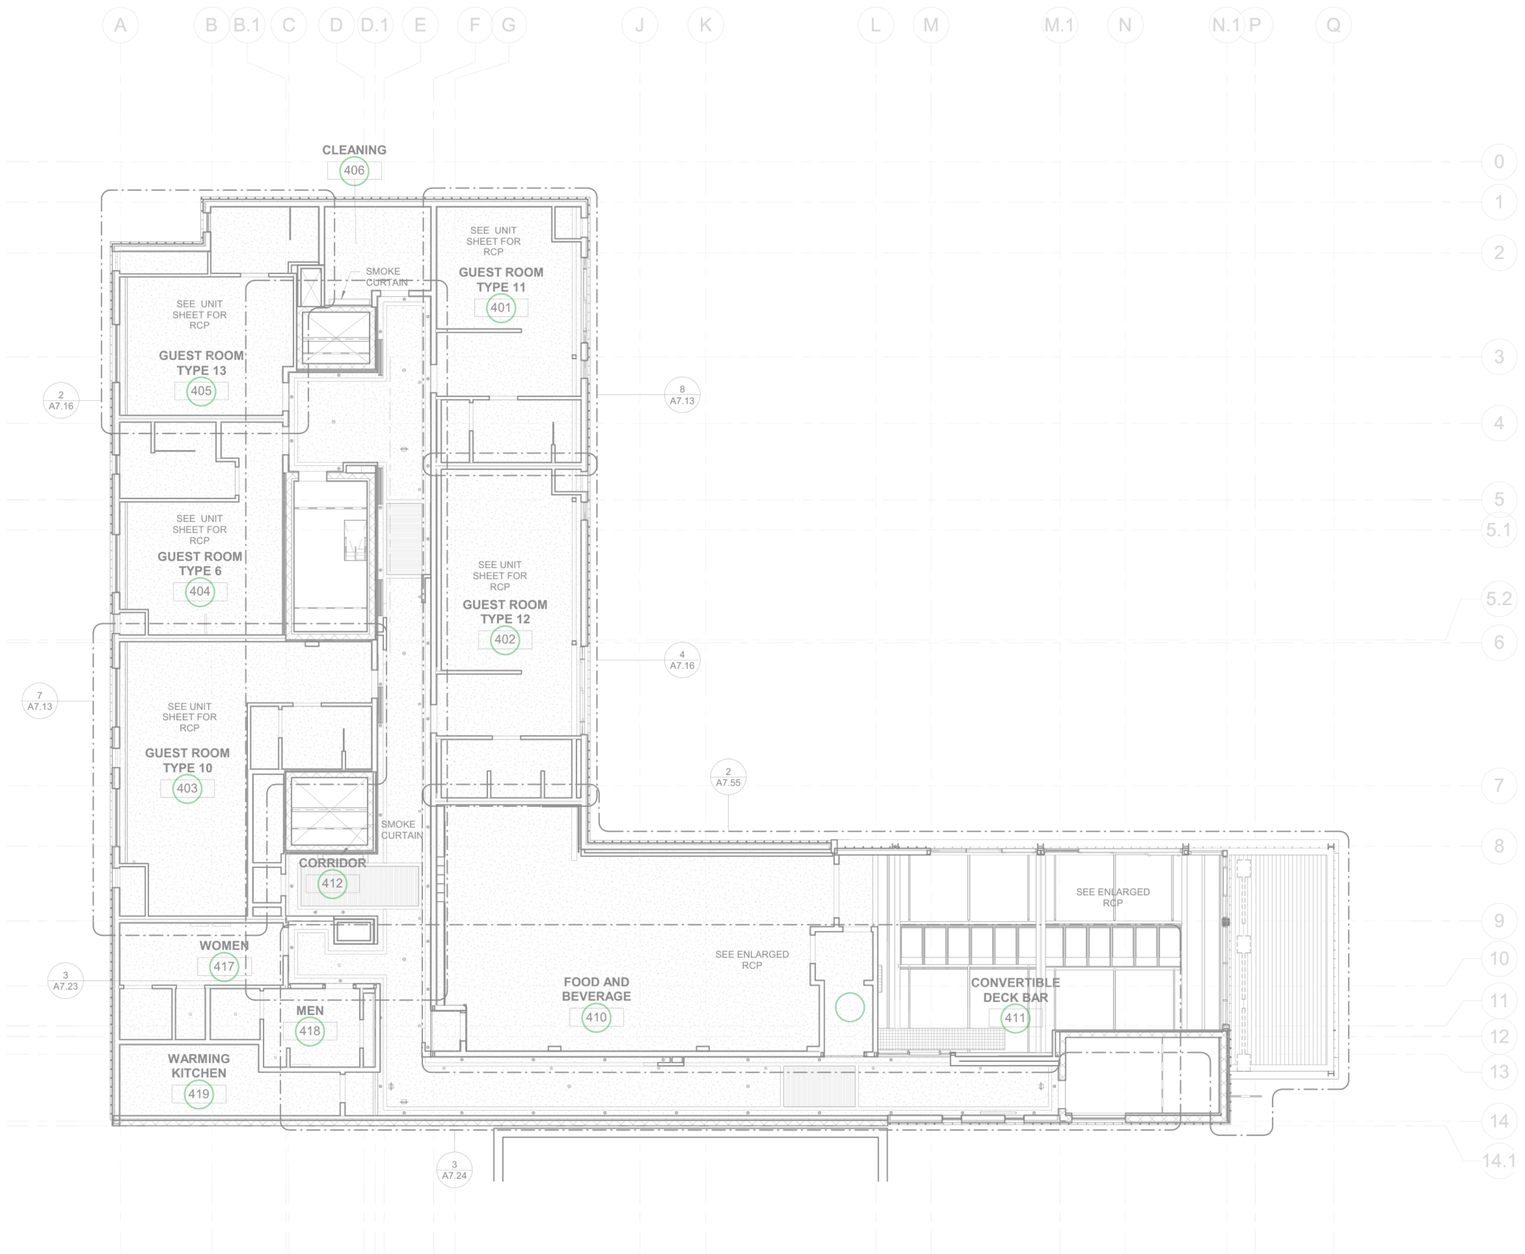

1 LEVEL 4 - RCP
1/8" = 1'-0"

CEILING LEGEND

CEILING TYPES:

ACT-1: 2X4 LAY-IN CEILING, PARKING

ACT-2: 2X2 LAY-IN CEILING, KITCHEN, BACK OF HOUSE

ACT-3: 2X2 LAY-IN CEILING, KITCHEN, WITH METAL FINISH

WS-1: WOOD SLAT CEILING. PRODUCT BY USG INTERIORS 'SPECIALTY CEILING SYSTEM', TRUE WOOD. WOOD VENEER COLOR SELECTED BY ARCHITECT, WITH BLACK FELT REVEAL BACKING. MILLWORK BORDERS AND FLAT PLANAR AREAS TO MATCH FINISH, MATERIAL, AND COLOR OF SLAT PRODUCT.

GYP-1: GYPSUM BOARD ON METAL SUSPENSION SYSTEM, OR WOOD FRAMING

GYP-2: GYPSUM BOARD CEILING, RATED 2-HOURS, AER-09038

NOTE: REFER TO LIGHTING PLANS FOR COMPLETE LAYOUTS AND SPECIFICATIONS OF LIGHTING FIXTURES. DIMENSIONED LOCATION TO BE PROVIDED BY ARCHITECT.

C:\Users\danielf\Documents\City Hotel-2024_1_dlipscomb74CJ8.rvt

4/22/2026 1:07:07 PM

HELTSHE

M1A MERIDIAN 105 ARCHITECTURE

CITY HOTEL
415 PERRY STREET, CASTLE ROCK, CO.

DATE: 4.22.2026
PROJ. NO. 2023.002


ISSUED FOR: PERMIT

SHEET TITLE: OVERALL RCP - LVL 4


SHEET NUMBER A3.04

TAKE-OFF LEGEND - A6.00 (partition schedule order)


- FW.1-0 - BOARD ONLY (WOOD FRAMING EXCLUDED) - 2 wall(s) - 18.79 LF
- FW.2-0 - BOARD ONLY (WOOD FRAMING EXCLUDED) - 1 wall(s) - 1.71 LF
- FW.4-0 - BOARD ONLY (WOOD FRAMING EXCLUDED) - 1 wall(s) - 2.93 LF

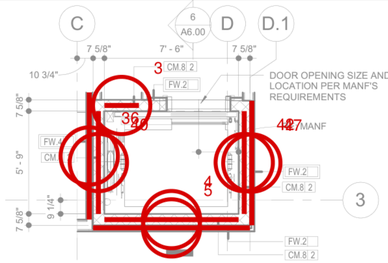


5 ENLARGED PLAN - SERVICE ELEVATOR - LVL 4
1/4" = 1'-0"

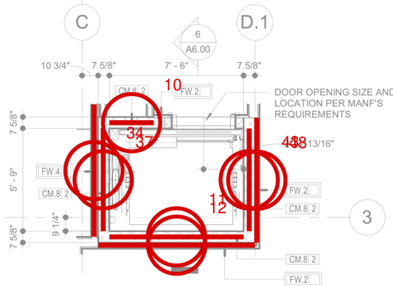


4 ENLARGED PLAN - SERVICE ELEVATOR - LVL 3
1/4" = 1'-0"

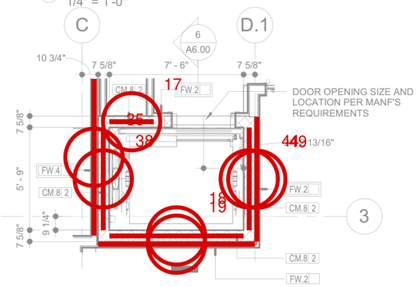


3 ENLARGED PLAN - SERVICE ELEVATOR - LVL 2
1/4" = 1'-0"

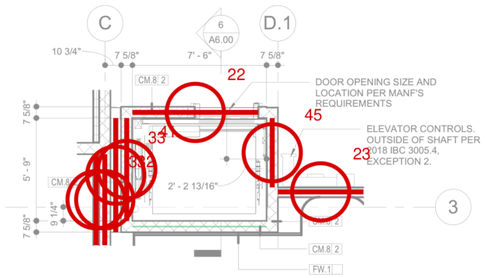


1 ENLARGED PLAN - SERVICE ELEVATOR - LVL 1
1/4" = 1'-0"

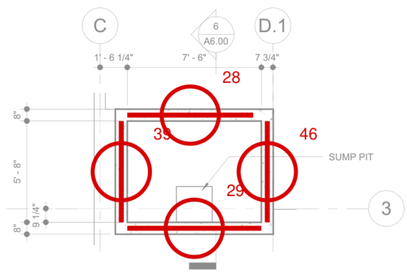


2 ENLARGED PLAN - SERVICE ELEVATOR PIT
1/4" = 1'-0"

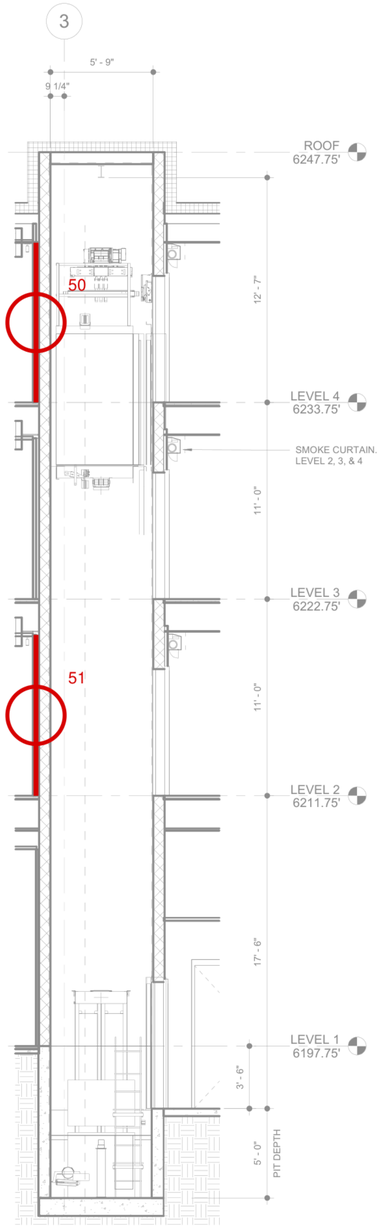


6 ENLARGED SECTION - SERVICE ELEVATOR
1/4" = 1'-0"

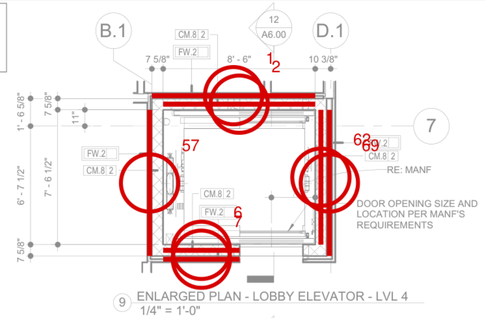


9 ENLARGED PLAN - LOBBY ELEVATOR - LVL 4
1/4" = 1'-0"

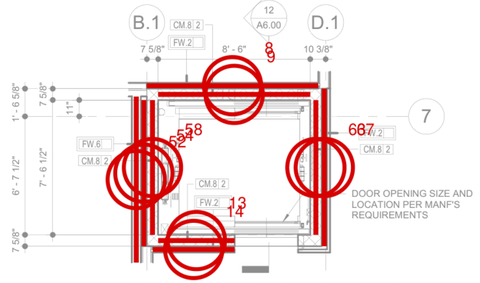


10 ENLARGED PLAN - LOBBY ELEVATOR - LVL 3
1/4" = 1'-0"

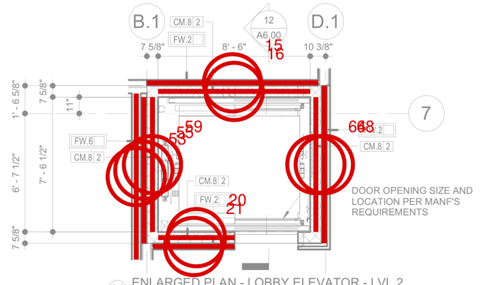


11 ENLARGED PLAN - LOBBY ELEVATOR - LVL 2
1/4" = 1'-0"

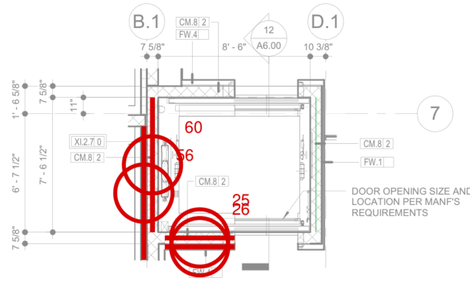

8 ENLARGED PLAN - LOBBY ELEVATOR - LVL 1
1/4" = 1'-0"

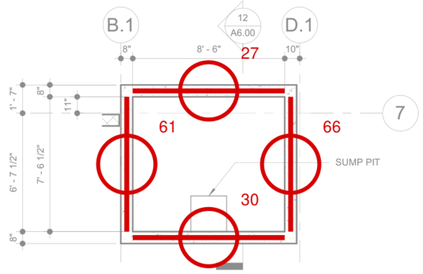

7 ENLARGED PLAN - LOBBY ELEVATOR PIT
1/4" = 1'-0"

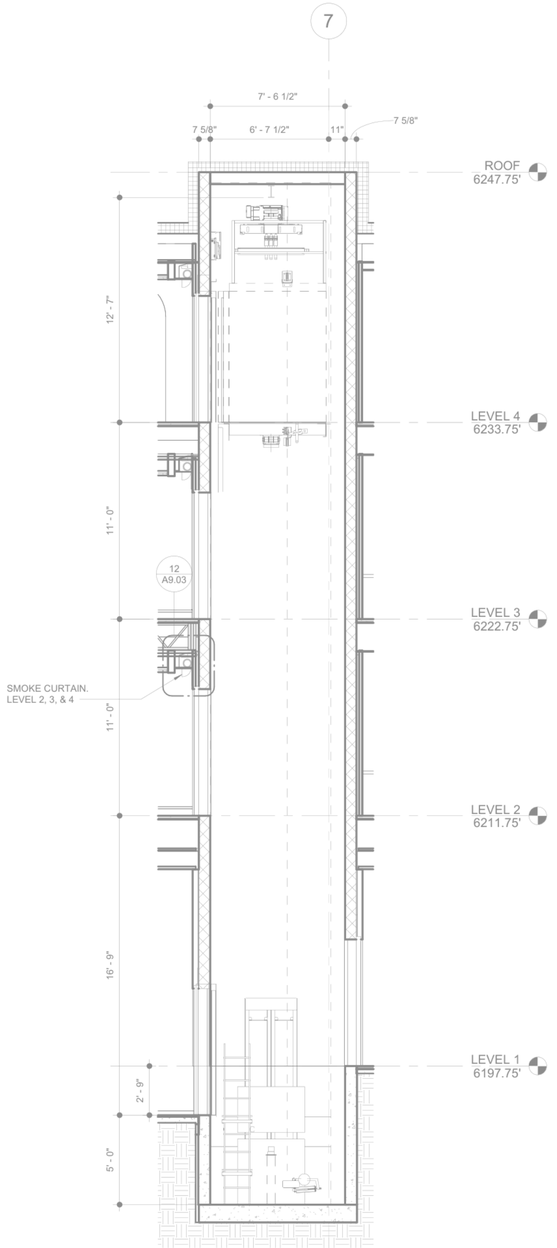

12 ENLARGED SECTION - LOBBY ELEVATOR
1/4" = 1'-0"

HELTSHE

M1A | MERIDIAN 105 ARCHITECTURE

CITY HOTEL

415 PERRY STREET, CASTLE ROCK, CO.

DATE: 4.22.2026	ISSUED FOR: PERMIT	SHEET TITLE: ELEVATOR PLANS & SECTIONS	SHEET NUMBER A6.00
PROJ. NO. 2023.002			


C:\Users\daniel\Documents\City Hotel-2024_1_dlipscomb74CJ8.rvt

4/22/2026 1:08:14 PM


TAKE-OFF LEGEND - A6.01 (gypsum board ceilings / soffits)

blue area = gyp bd ceiling (ceilings), green area / line = gyp bd ceiling / soffit of the misc rows (CLG / SOF / RS / CAN / BW): 1 items, 74.90 SF (Contents: board · ceiling tag · room · SF · ceiling height · detail · id)


measure: /Measure at the printed scale of the sheet; SF = Excel row (ceiling id)

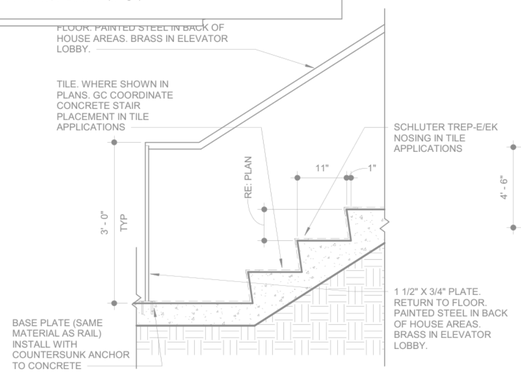

1 CONCRETE STAIR SECTION
3/4" = 1'-0"

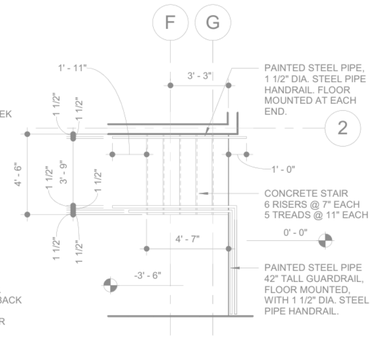


2 ENLARGED PLAN - NORTH RAMP - LVL 1
1/4" = 1'-0"

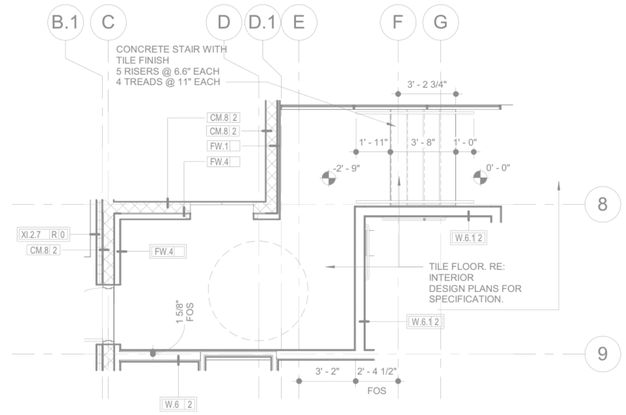


3 ENLARGED PLAN - LOBBY SERVICE STAIR - LVL 1
1/4" = 1'-0"

STAIRS - GENERAL NOTES


1. ALL OVERALL STAIR ENCLOSURE DIMENSIONS ARE TO FACE OF FINISH U.O.N.
2. ALL HANDRAIL EXTENSIONS AT WALL ARE TO BE EQUAL TO STAIR TREAD AT BASE OF STAIR RUN AND 1'-0" AT TOP OF STAIR RUN PER CODE.
3. ALL HANDRAILS AT WALL TO BE 1-1/2" DIA. PIPE RAIL AND LOCATED 1-1/2" AWAY FROM FINISHED FACE OF WALL PER CODE.

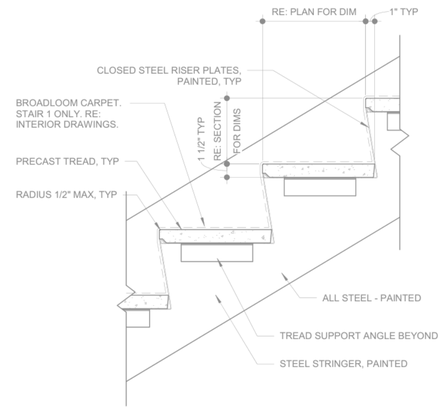


4 STAIR TREAD PRECAST
1 1/2" = 1'-0"

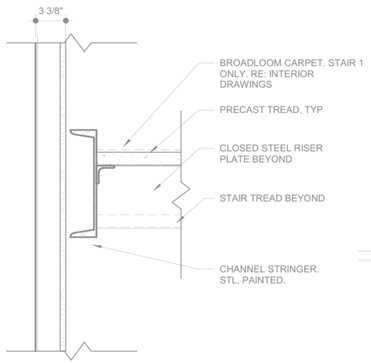


5 STAIR STRINGER
1 1/2" = 1'-0"

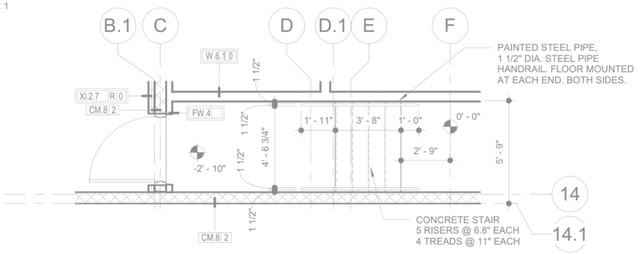


6 ENLARGED PLAN - RETAIL SERVICE STAIR - LVL 1
1/4" = 1'-0"

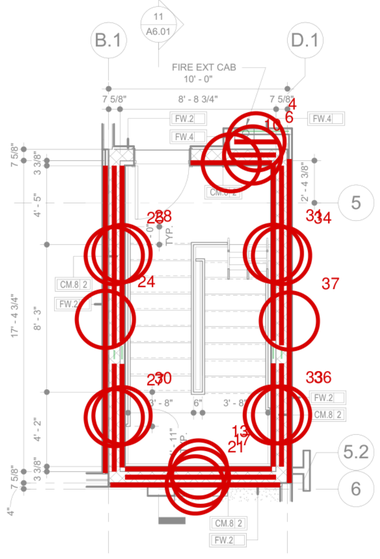


7 ENLARGED PLAN - LOBBY STAIR - LVL 4
1/4" = 1'-0"

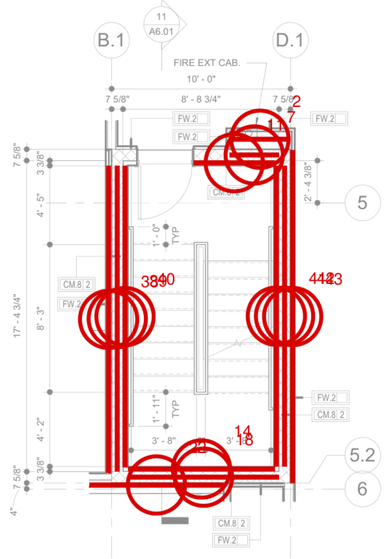


8 ENLARGED PLAN - LOBBY STAIR - LVL 3
1/4" = 1'-0"

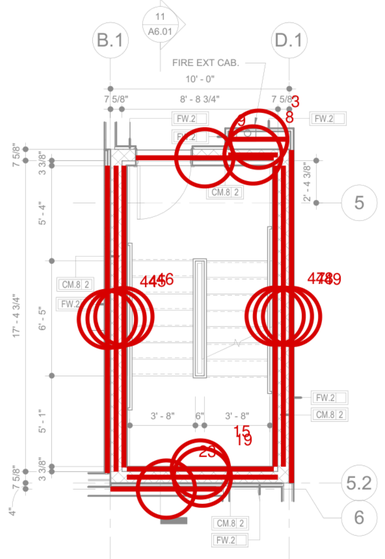

9 ENLARGED PLAN - LOBBY STAIR - LVL 2
1/4" = 1'-0"

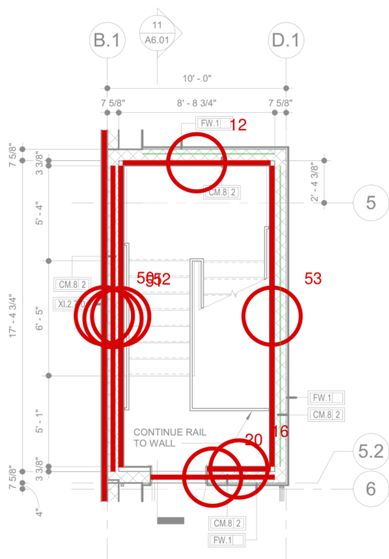


10 ENLARGED PLAN - LOBBY STAIR - LVL 1
1/4" = 1'-0"

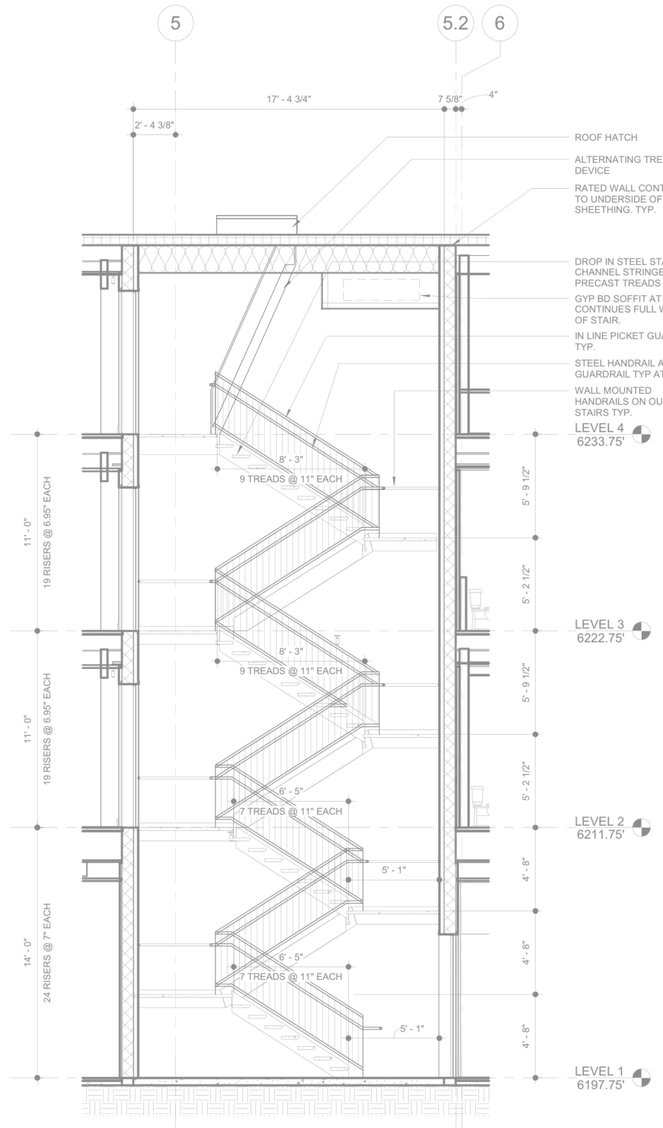


11 ENLARGED SECTION - LOBBY STAIR
1/4" = 1'-0"

TAKE-OFF LEGEND - A6.02 (partition schedule order)


- FI.2-0 - BOARD ONLY (WOOD FRAMING EXCLUDED) - 5 wall(s) - 51.52 LF
- FW.1-0 - BOARD ONLY (WOOD FRAMING EXCLUDED) - 1 wall(s) - 1.64 LF

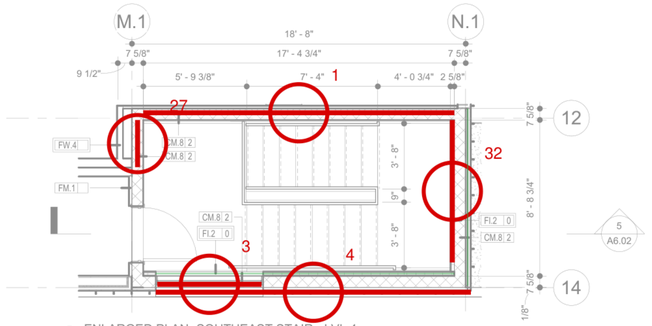


4 ENLARGED PLAN -SOUTHEAST STAIR - LVL 4
1/4" = 1'-0"

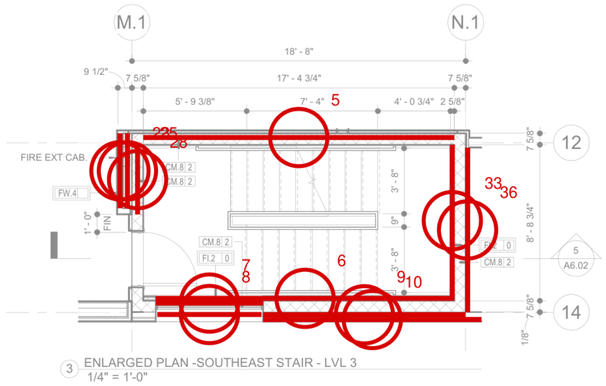

3 ENLARGED PLAN -SOUTHEAST STAIR - LVL 3
1/4" = 1'-0"

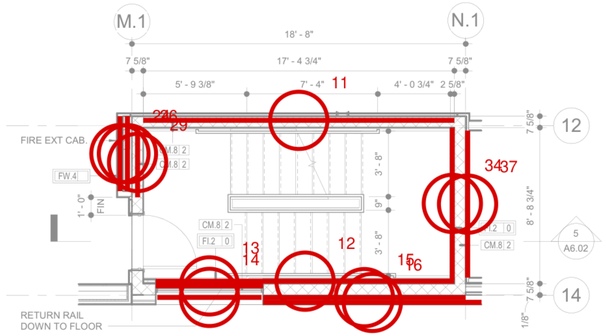


2 ENLARGED PLAN -SOUTHEAST STAIR - LVL 2
1/4" = 1'-0"

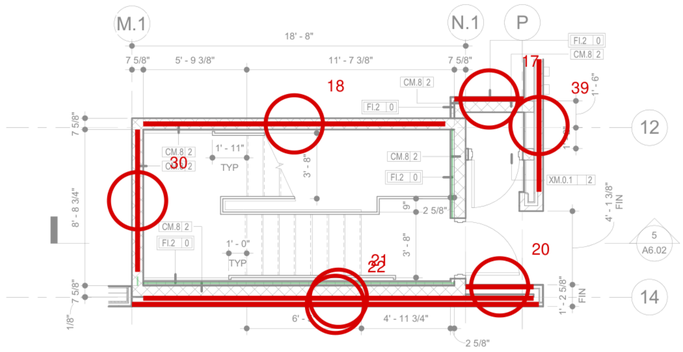

1 ENLARGED PLAN -SOUTHEAST STAIR - LVL 1
1/4" = 1'-0"

STAIRS - GENERAL NOTES

1. ALL OVERALL STAIR ENCLOSURE DIMENSIONS ARE TO FACE OF FINISH U.O.N.
2. ALL HANDRAIL EXTENSIONS AT WALL ARE TO BE EQUAL TO STAIR TREAD AT BASE OF STAIR RUN AND 1'-0" AT TOP OF STAIR RUN PER CODE.
3. ALL HANDRAILS AT WALL TO BE 1-1/2" DIA. PIPE RAIL AND LOCATED 1-1/2" AWAY FROM FINISHED FACE OF WALL PER CODE.

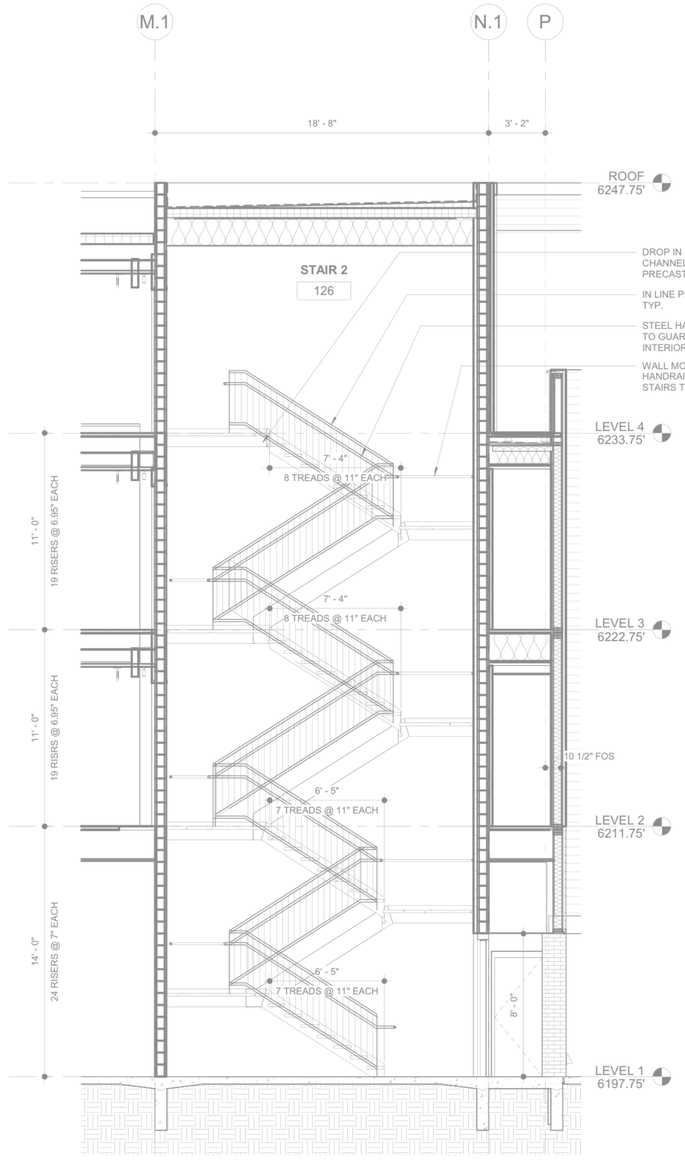

5 ENLARGED SECTION - SOUTHEAST STAIR
1/4" = 1'-0"

C:\Users\daniel\Documents\City Hotel-2024_1_dlipscomb74CJ8.rvt
4/22/2026 1:08:24 PM

HELTSHE

M1A MERIDIAN 105 ARCHITECTURE

CITY HOTEL
415 PERRY STREET, CASTLE ROCK, CO.

DATE: 4.22.2026	ISSUED FOR: PERMIT	SHEET TITLE: SOUTHEAST STAIR PLANS & SECTIONS	SHEET NUMBER A6.02
PROJ. NO. 2023.002			


TAKE-OFF LEGEND - A7.30 (partition schedule order)

- Fl.2-0 - BOARD ONLY (WOOD FRAMING EXCLUDED) - 2 wall(s) - 11.67 LF
- FW.4-0 - BOARD ONLY (WOOD FRAMING EXCLUDED) - 2 wall(s) - 12.92 LF
- W.6-0 - BOARD ONLY (WOOD FRAMING EXCLUDED) - 10 wall(s) - 118.71 LF


TAKE-OFF LEGEND - A7.30 (gypsum board ceilings / soffits)

blue area = gyp bd ceiling (ceilings), green area / line = gyp bd ceiling / soffit of the misc rows (CLG / SOF / RS / CAN / BW): 3 items, 168.53 SF (Contents: board · ceiling tag · room · SF · ceiling height · detail · id)


measure::/Measure at the printed scale of the sheet; SF = Excel row (ceiling id)

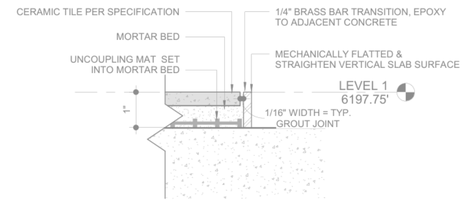


2 SECTION DETAIL - TILE / CONCRETE TRANSITION
6" = 1'-0"

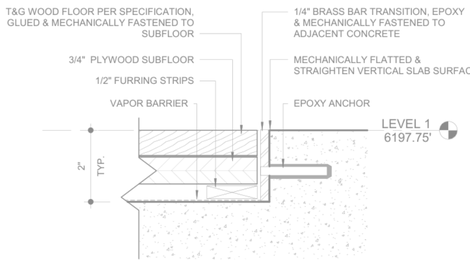

3 SECTION DETAIL - WOOD / CONCRETE TRANSITION
6" = 1'-0"

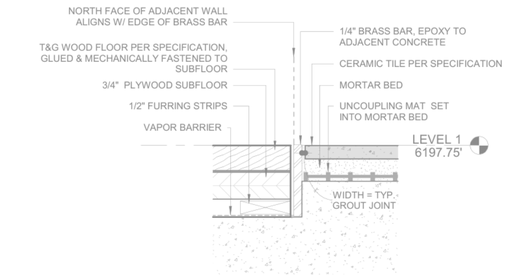

4 SECTION DETAIL - WOOD / TILE TRANSITION
6" = 1'-0"

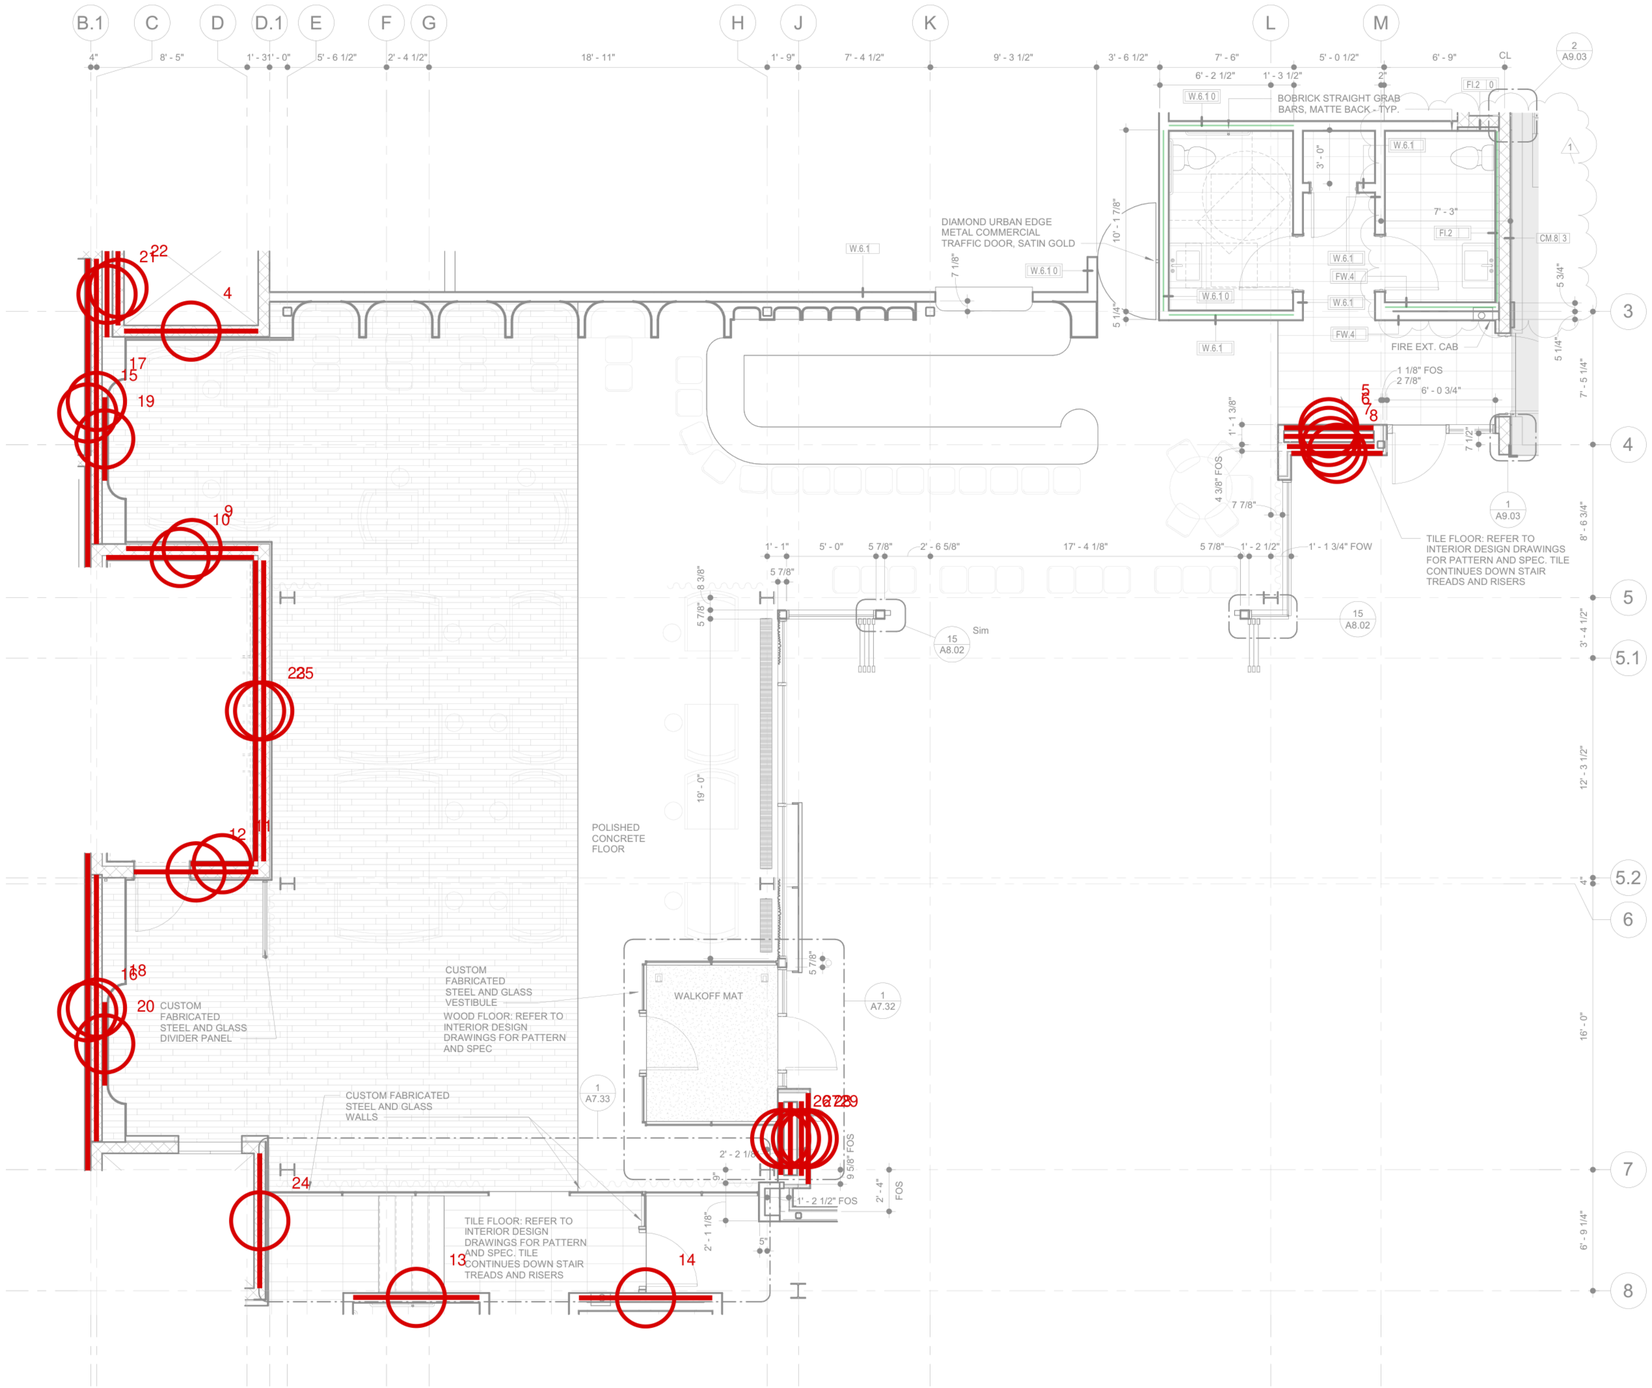

1 ENLARGEDPLAN - LOBBY & BAR
1/4" = 1'-0"

C:\Users\daniel\Documents\City Hotel-2024_1_dlipscomb74CJ8.rvt

4/22/2026 1:09:20 PM


HELTSHE

M1A MERIDIAN 105 ARCHITECTURE


CITY HOTEL

415 PERRY STREET, CASTLE ROCK, CO.


DATE: 4.22.2026	ISSUED FOR: PERMIT	SHEET TITLE: LOBBY - ENLARGED PLANS	SHEET NUMBER A7.30
PROJ. NO. 2023.002			

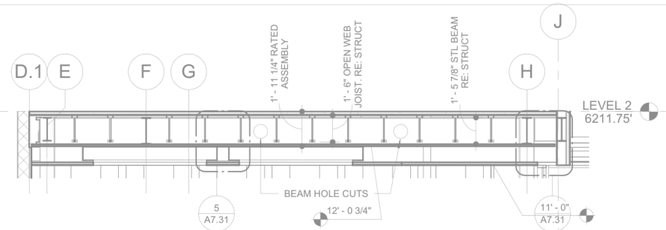


2 SECTION - LOBBY CEILING EAST WEST
1/4" = 1'-0"

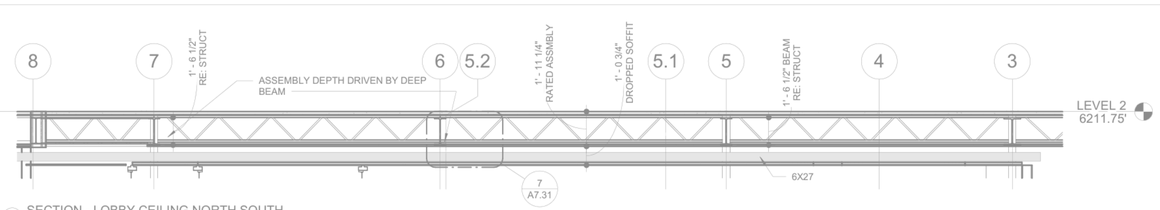

4 SECTION - LOBBY CEILING NORTH SOUTH
1/4" = 1'-0"

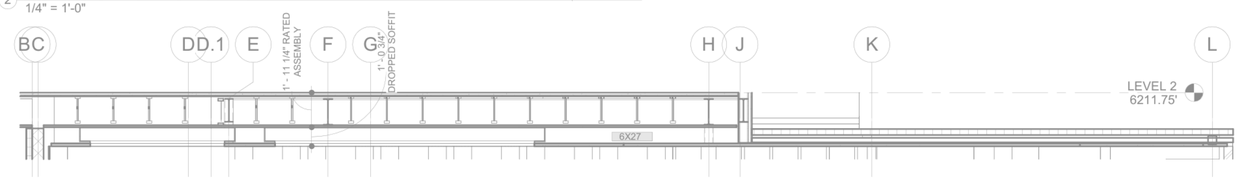


3 SECTION - BAR CEILING EAST WEST
1/4" = 1'-0"

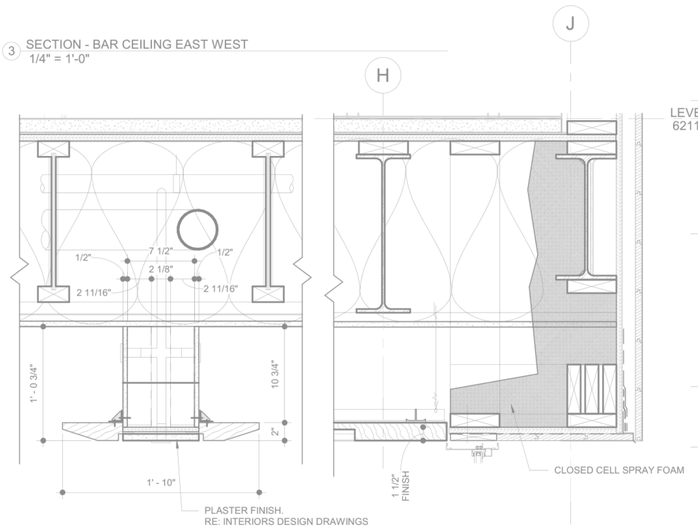


5 DETAIL - LOBBY CEILING
1 1/2" = 1'-0"

6 DETAIL - LOBBY CEILING EXT
1 1/2" = 1'-0"

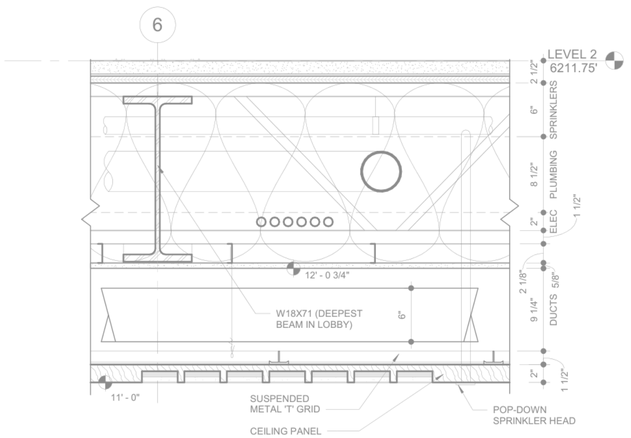

7 SECTION - LOBBY CEILING DETAIL
1 1/2" = 1'-0"

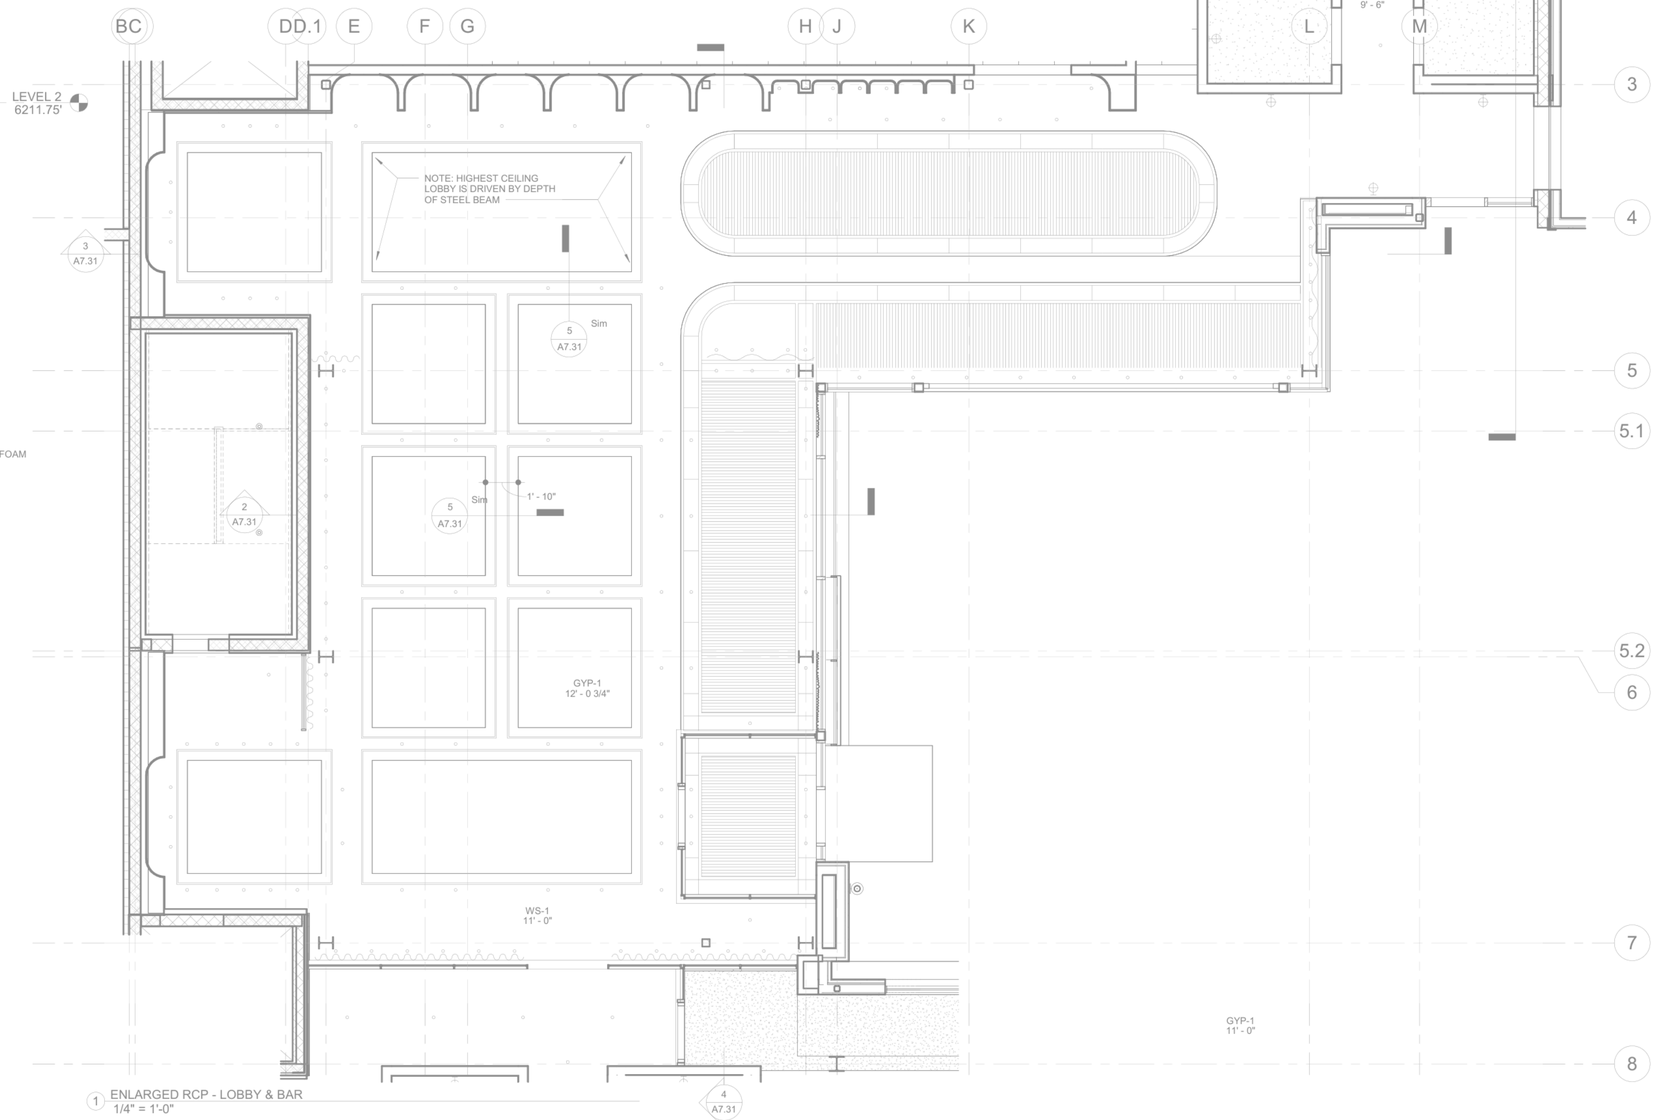

1 ENLARGED RCP - LOBBY & BAR
1/4" = 1'-0"

CEILING LEGEND

CEILING TYPES:

ACT-1: 2X4 LAY-IN CEILING, PARKING

ACT-2: 2X2 LAY-IN CEILING, KITCHEN, BACK OF HOUSE

ACT-3: 2X2 LAY-IN CEILING, KITCHEN, WITH METAL FINISH

WS-1: WOOD SLAT CEILING. PRODUCT BY USG INTERIORS 'SPECIALTY CEILING SYSTEM', TRUE WOOD. WOOD VENEER COLOR SELECTED BY ARCHITECT, WITH BLACK FELT REVEAL BACKING. MILLWORK BORDERS AND FLAT PLANAR AREAS TO MATCH FINISH, MATERIAL, AND COLOR OF SLAT PRODUCT.

GYP-1: GYPSUM BOARD ON METAL SUSPENSION SYSTEM, OR WOOD FRAMING

GYP-2: GYPSUM BOARD CEILING, RATED 2-HOURS, AER-09038

NOTE: REFER TO LIGHTING PLANS FOR COMPLETE LAYOUTS AND SPECIFICATIONS OF LIGHTING FIXTURES. DIMENSIONED LOCATION TO BE PROVIDED BY ARCHITECT.

C:\Users\daniel\Documents\City Hotel-2024_1_dljpscomb74CJ8.rvt
4/22/2026 1:09:25 PM

HELTSHE

M1A MERIDIAN 105 ARCHITECTURE

415 PERR

TAKE-OFF LEGEND - A7.31 (gypsum board ceilings / soffits)
blue area = gyp bd ceiling (ceilings), green area / line = gyp bd ceiling / soffit of the misc rows (CLG / SOF / RS / CAN / BW): 5 items, 1,162 SF (Contents: board - ceiling tag - room - SF - ceiling height - detail - id)
measure: /Measure at the printed scale of the sheet; SF = Excel row (ceiling id)

DATE: 4.22.2026
PROJ. NO. 2023.002


ISSUED FOR: PERMIT

SHEET TITLE: LOBBY - ENLARGED REFLECTED CEILING PLAN


SHEET NUMBER
A7.31

TAKE-OFF LEGEND - A7.45 (partition schedule order)


- FI.2-0 - BOARD ONLY (WOOD FRAMING EXCLUDED) - 2 wall(s) - 21.25 LF
- FI.6-0 - BOARD ONLY (WOOD FRAMING EXCLUDED) - 1 wall(s) - 8.63 LF
- W.6-0 - BOARD ONLY (WOOD FRAMING EXCLUDED) - 1 wall(s) - 22.80 LF
- W.6-1 - BOARD ONLY (WOOD FRAMING EXCLUDED) - 2 wall(s) - 21.25 LF

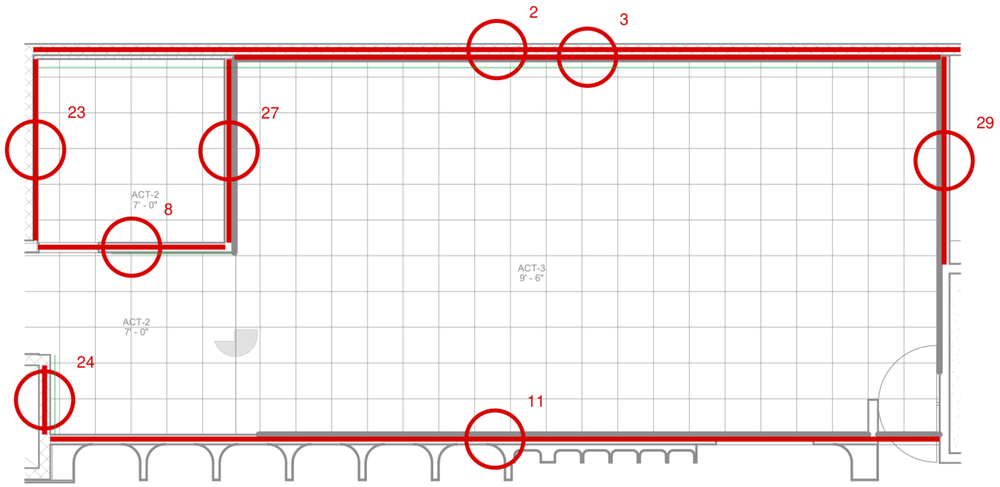


4 ENLARGED RCP - LOBBY REST ROOMS
1/4" = 1'-0"

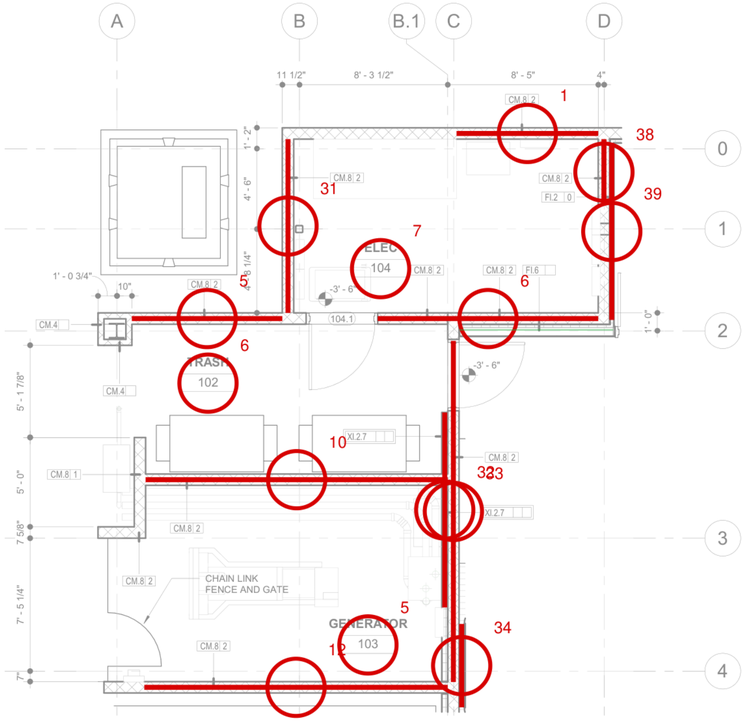

3 ENLARGED PLAN - TRASH & SERVICE ENTRANCE
1/4" = 1'-0"

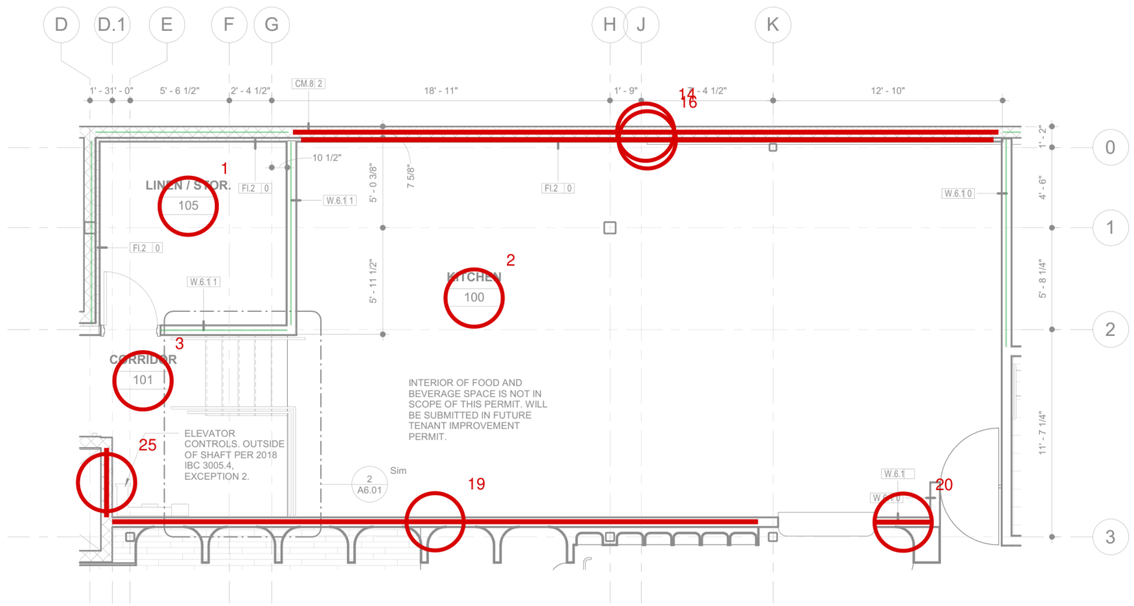

1 ENLARGED PLAN - LOBBY RESTROOMS
1/4" = 1'-0"

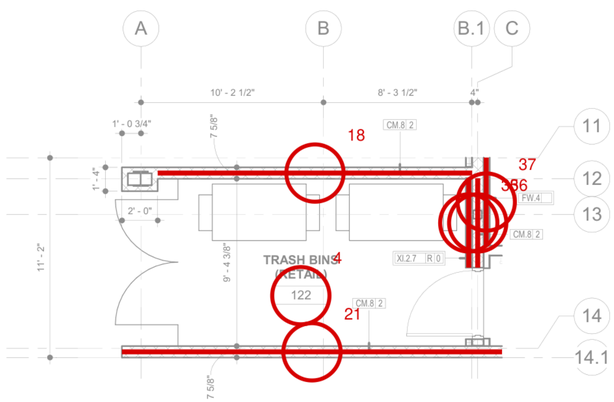

2 ENLARGED PLAN - RETAIL TRASH
1/4" = 1'-0"

CEILING LEGEND

CEILING TYPES:

ACT-1: 2X4 LAY-IN CEILING, PARKING

ACT-2: 2X2 LAY-IN CEILING, KITCHEN, BACK OF HOUSE

ACT-3: 2X2 LAY-IN CEILING, KITCHEN, WITH METAL FINISH

WS-1: WOOD SLAT CEILING. PRODUCT BY USG INTERIORS 'SPECIALTY CEILING SYSTEM', TRUE WOOD. WOOD VENEER COLOR SELECTED BY ARCHITECT, WITH BLACK FELT REVEAL BACKING. MILLWORK BORDERS AND FLAT PLANAR AREAS TO MATCH FINISH, MATERIAL, AND COLOR OF SLAT PRODUCT.

GYP-1: GYPSUM BOARD ON METAL SUSPENSION SYSTEM, OR WOOD FRAMING

GYP-2: GYPSUM BOARD CEILING, RATED 2-HOURS, AER-09038

NOTE: REFER TO LIGHTING PLANS FOR COMPLETE LAYOUTS AND SPECIFICATIONS OF LIGHTING FIXTURES. DIMENSIONED LOCATION TO BE PROVIDED BY ARCHITECT.

HELTSHE

M1A MERIDIAN 105 ARCHITECTURE

CITY HOTEL

415 PERRY STREET, CASTLE ROCK, CO.

DATE: 4.22.2026
PROJ. NO. 2023.002
ISSUED FOR: PERMIT
SHEET TITLE: KITCHEN, UTILITY, TRASH AREAS - ENLARGED PLANS AND RCPS

SHEET NUMBER
A7.45

C:\Users\daniel\Documents\City Hotel-2024_1_dlipscomb74CJB.rvt

4/22/2026 1:09:37 PM


TAKE-OFF LEGEND - A7.50 (partition schedule order)

- CH.6-2 - SHAFT WALL (C-H STUDS AND J-RUNNER IN THE MATERIAL SUMMARY) - 16 wall(s) - 51.92 LF
- DW.4-1 - BOARD ONLY (WOOD FRAMING EXCLUDED) - 2 wall(s) - 36.50 LF
- FW.4-0 - BOARD ONLY (WOOD FRAMING EXCLUDED) - 9 wall(s) - 51.82 LF
- W.4-0 - BOARD ONLY (WOOD FRAMING EXCLUDED) - 5 wall(s) - 43.60 LF
- W.6-0 - BOARD ONLY (WOOD FRAMING EXCLUDED) - 18 wall(s) - 168.82 LF
- W.6-1 - BOARD ONLY (WOOD FRAMING EXCLUDED) - 6 wall(s) - 50.89 LF
- W.6-2 - BOARD ONLY (WOOD FRAMING EXCLUDED) - 26 wall(s) - 166.74 LF


TAKE-OFF LEGEND - A7.50 (gypsum board ceilings / soffits)

blue area = gyp bd ceiling (ceilings), green area / line = gyp bd ceiling / soffit of the misc rows (CLG / SOF / RS / CAN / BW): 6 items, 404.43 SF (Ceiling Height : ceiling tag - room : SF : ceiling height : detail - id)


measure::Measure at the printed scale of the sheet; SF = Excel row (ceiling id)

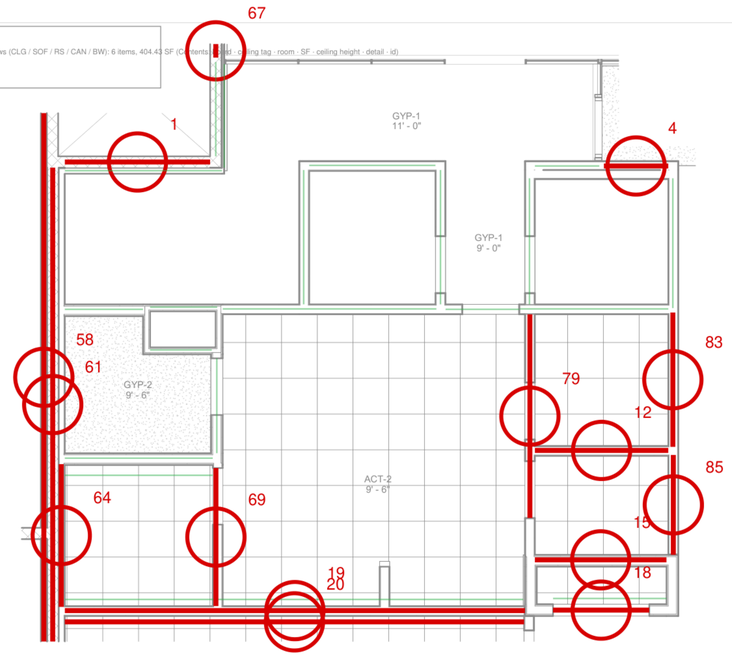

2 ENLARGED RCP -STAFF & SERVICE
1/4" = 1'-0"

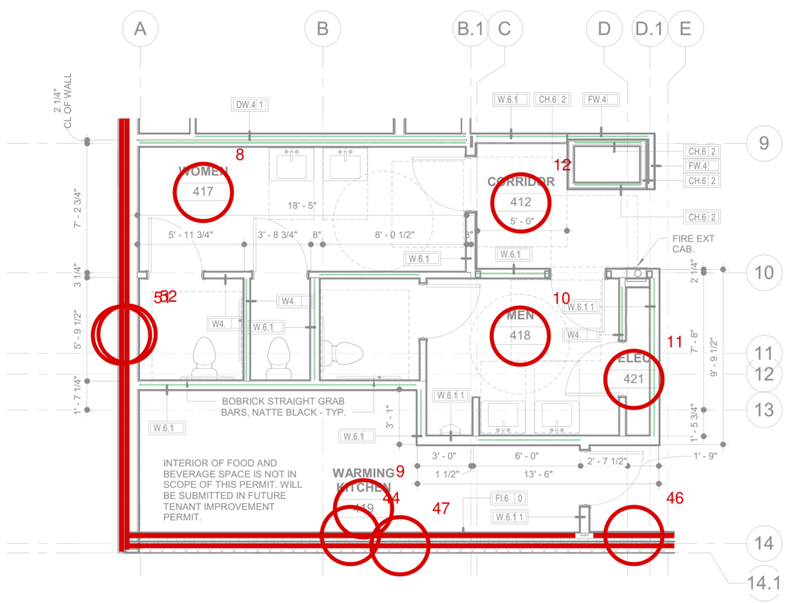

3 ENLARGED PLAN LVL 4 BATHROOMS
1/4" = 1'-0"

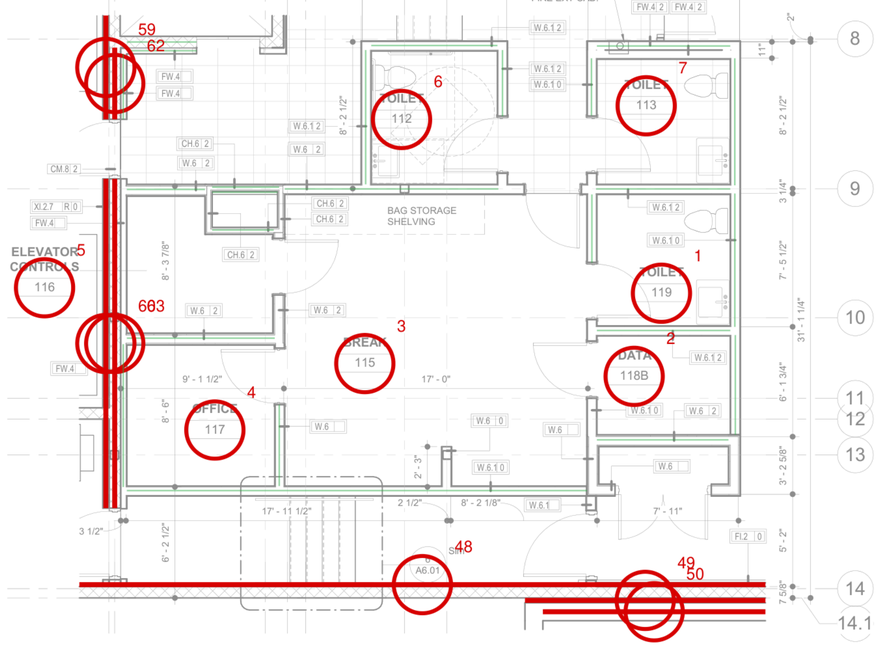

1 ENLARGED PLAN -STAFF & SERVICE
1/4" = 1'-0"

CEILING LEGEND

CEILING TYPES:

ACT-1: 2X4 LAY-IN CEILING, PARKING

ACT-2: 2X2 LAY-IN CEILING, KITCHEN, BACK OF HOUSE

ACT-3: 2X2 LAY-IN CEILING, KITCHEN, WITH METAL FINISH

WS-1: WOOD SLAT CEILING. PRODUCT BY USG INTERIORS 'SPECIALTY CEILING SYSTEM', TRUE WOOD. WOOD VENEER COLOR SELECTED BY ARCHITECT, WITH BLACK FELT REVEAL BACKING. MILLWORK BORDERS AND FLAT PLANAR AREAS TO MATCH FINISH, MATERIAL, AND COLOR OF SLAT PRODUCT.

GYP-1: GYPSUM BOARD ON METAL SUSPENSION SYSTEM, OR WOOD FRAMING

GYP-2: GYPSUM BOARD CEILING, RATED 2-HOURS, AER-09038

NOTE: REFER TO LIGHTING PLANS FOR COMPLETE LAYOUTS AND SPECIFICATIONS OF LIGHTING FIXTURES. DIMENSIONED LOCATION TO BE PROVIDED BY ARCHITECT.

C:\Users\daniel\Documents\City Hotel-2024_1_dlipscomb74CJ8.rvt
4/22/2026 1:09:41 PM

HELTSHE

M1A MERIDIAN 105 ARCHITECTURE


CITY HOTEL
415 PERRY STREET, CASTLE ROCK, CO.

DATE: 4.22.2026
PROJ. NO. 2023.002
ISSUED FOR: PERMIT
SHEET TITLE: LEVEL 4 RESTROOM, LEVEL 1 STAFF AREAS, PLANS AND RCPS


SHEET NUMBER
A7.50

TAKE-OFF LEGEND - A7.55 (partition schedule order)

W.6-1 - BOARD ONLY (WOOD FRAMING EXCLUDED) - 4 wall(s) - 34.19 LF

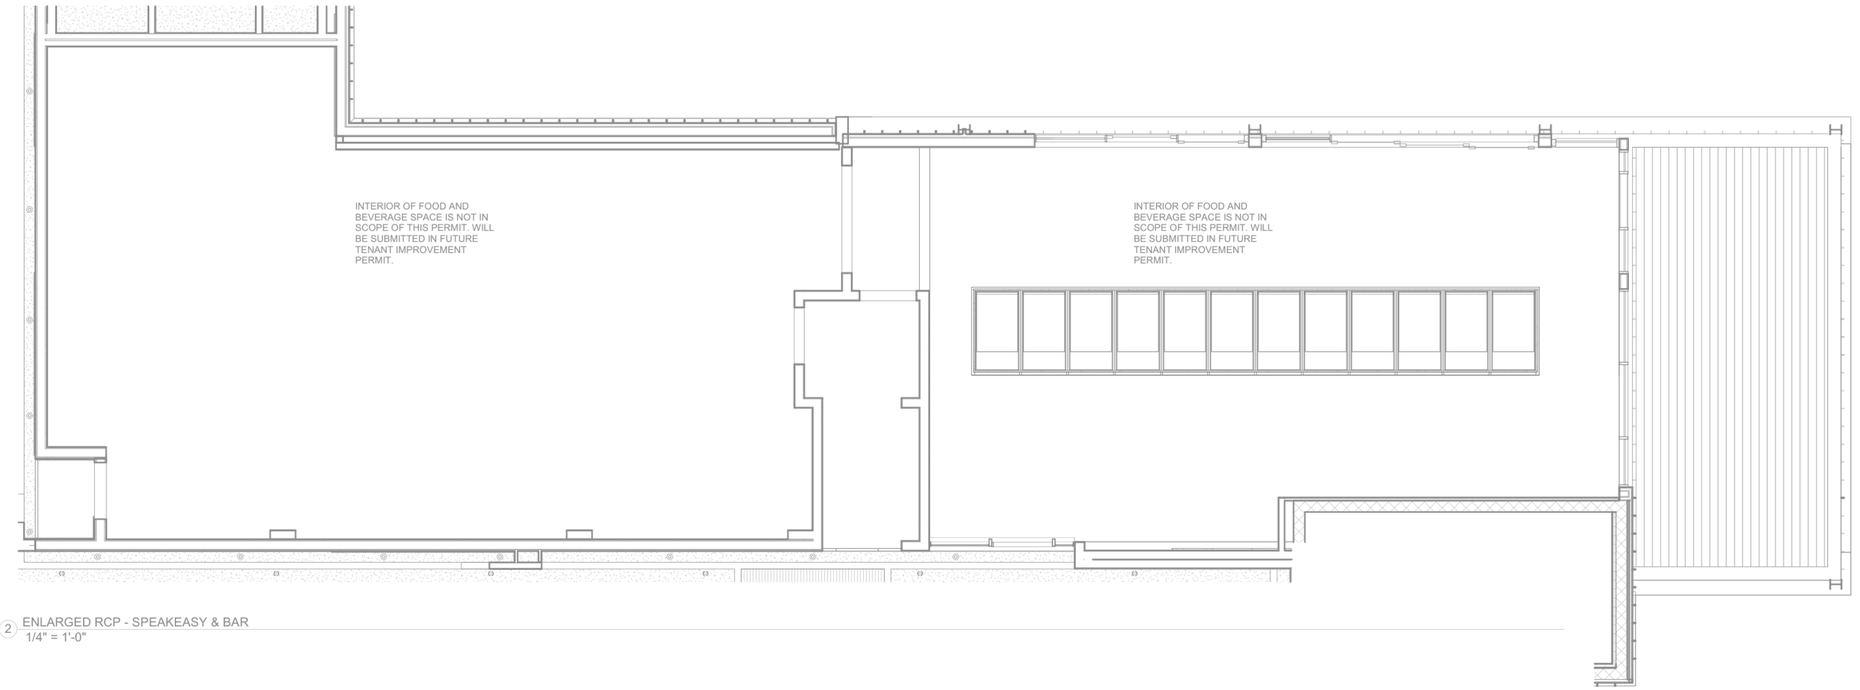

2 ENLARGED RCP - SPEAKEASY & BAR
1/4" = 1'-0"

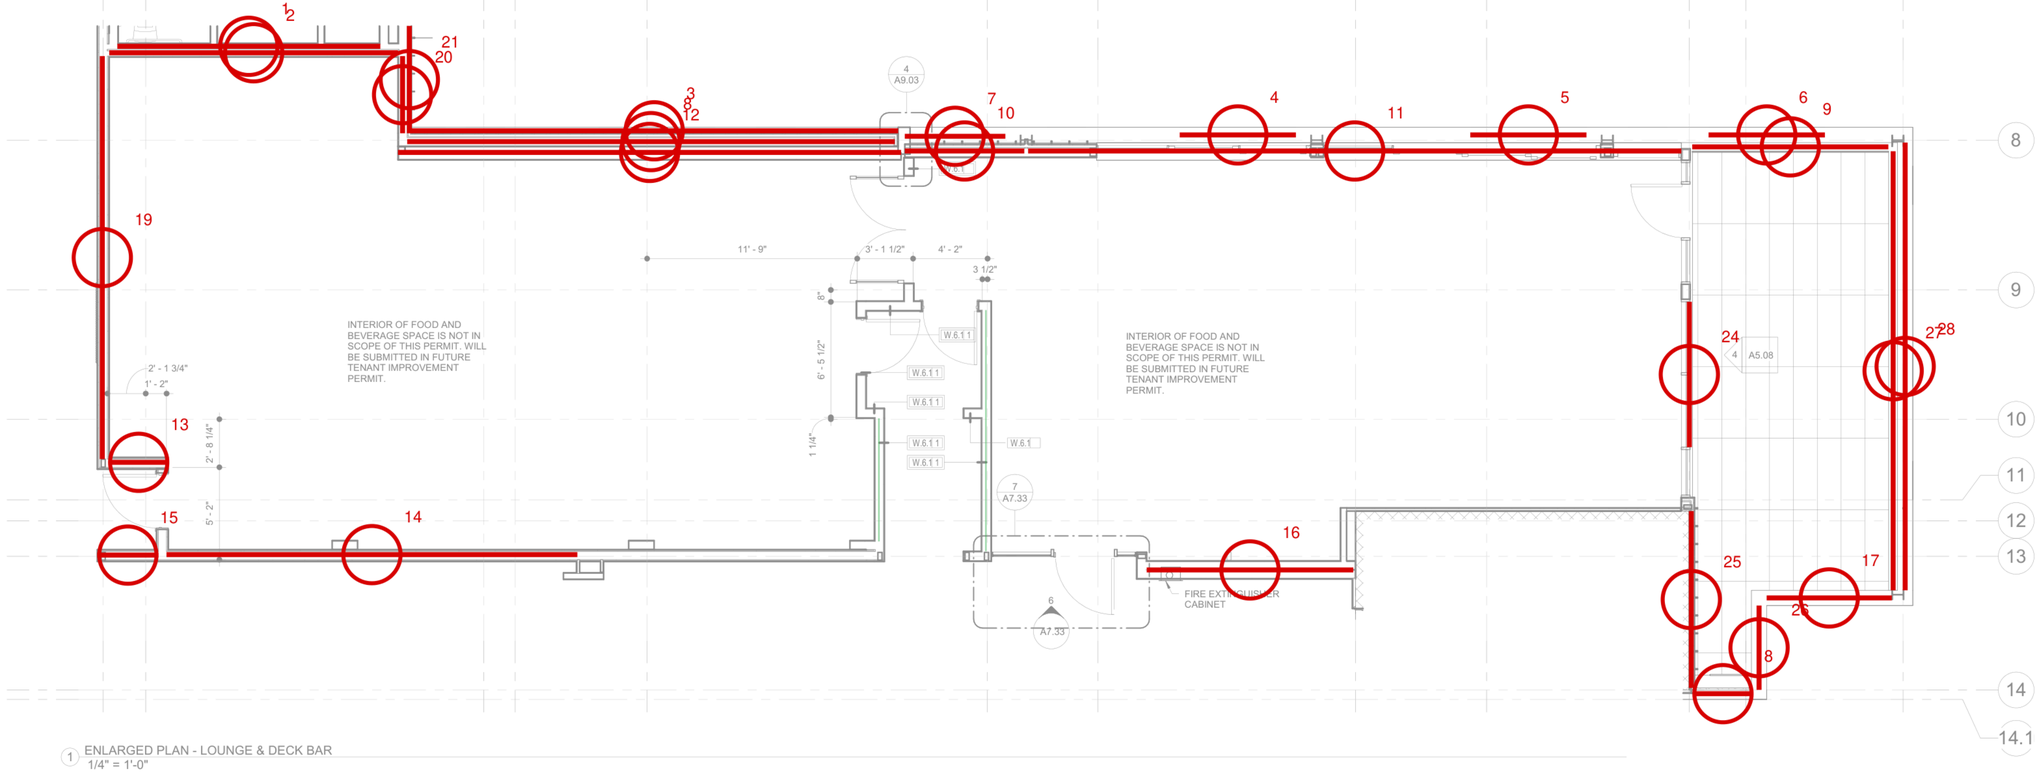

1 ENLARGED PLAN - LOUNGE & DECK BAR
1/4" = 1'-0"

HELTSHE

M1A | MERIDIAN 105 ARCHITECTURE

CITY HOTEL

415 PERRY STREET, CASTLE ROCK, CO.

DATE: 4.22.2026
PROJ. NO. 2023.002

ISSUED FOR: PERMIT

SHEET TITLE: LEVEL 4 FOOD AND BEVERAGE SPACES - ENLARGED PLAN AND RCP

SHEET NUMBER A7.55

C:\Users\daniel\Documents\City Hotel-2024_1_dlipscomb74CJ8.rvt

4/22/2026 1:09:44 PM